
# ПдСх / входи

Плита 1192×1250 мм · шов 8 мм · справа 792 мм | 1:125, А3 без масштабування


Рядова сітка: 1250 + 8 = 1258 мм. Ряди не збігаються автоматично з поверхами.

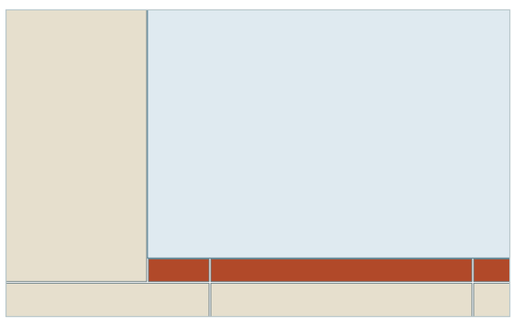



**SE-003: 277×103 мм / 1:28**



**SE-016: 1192×103 мм / 1:28**

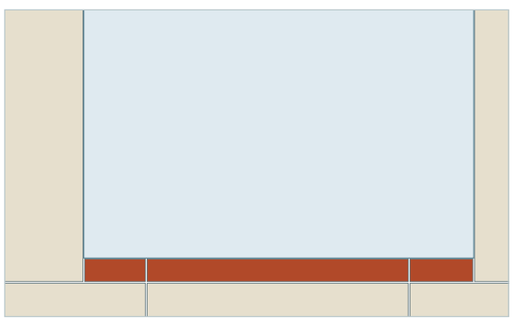

**SE-025: 287×103 мм / 1:28**

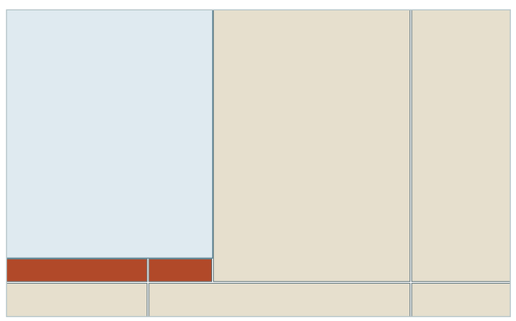

**33 × 1192 + 792 + 33 × 8 + 4 + 4 = 40400 мм**

449 деталей · 302.91 м²

Висота: 7 × 1250 + 661 + 7 × 8 + 4 + 4 = 9475 мм


Попереджень стіни: 36 · всі IDs у JSON

Номери у плитах: SE-NNN. Помаранчеві частини утримані від різання; перелік на арк.05.


# ПнЗх / балкони

Плита 1192×1250 мм · шов 8 мм · справа 792 мм | 1:125, А3 без масштабування


Рядова сітка: 1250 + 8 = 1258 мм. Ряди не збігаються автоматично з поверхами.

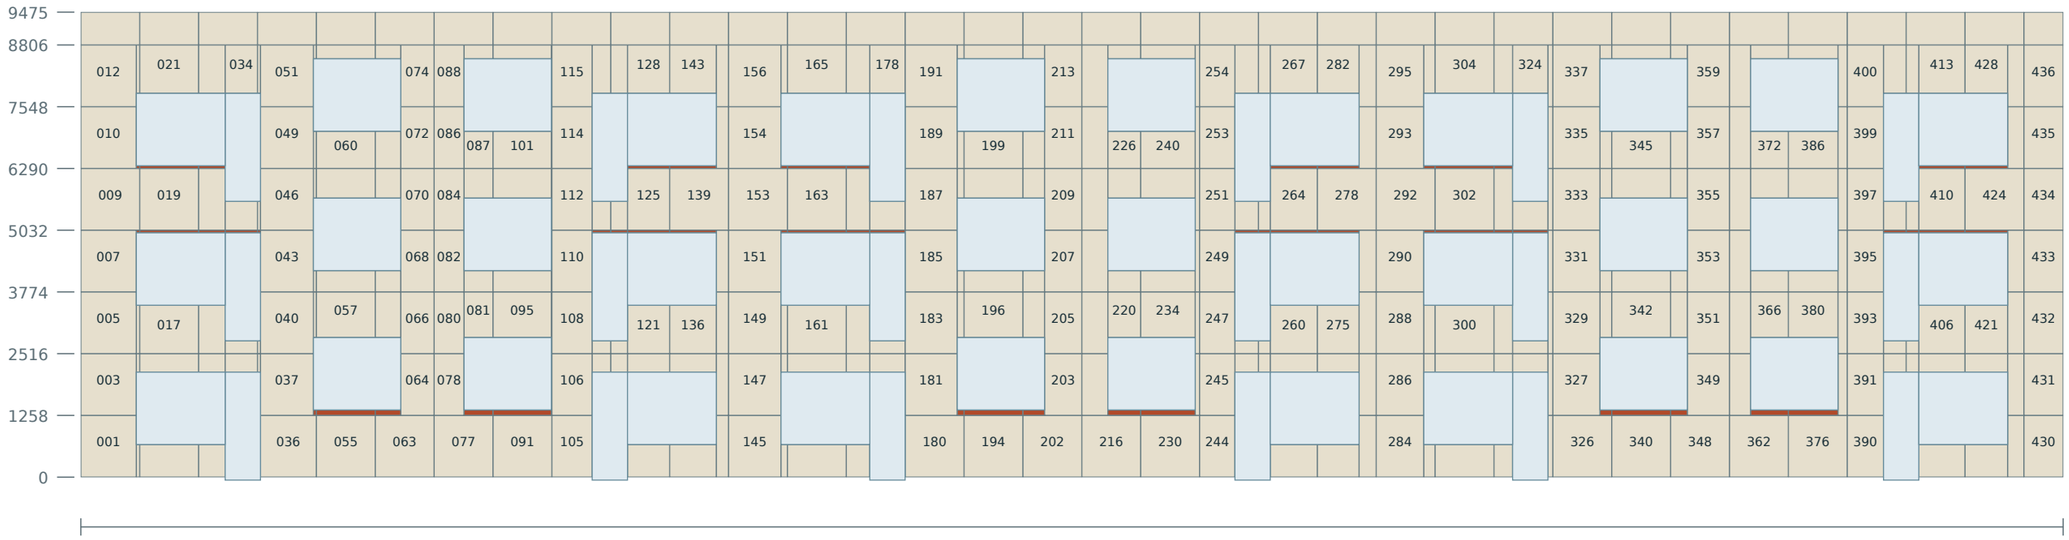



**NW-008: 61×46 мм / 1:28**

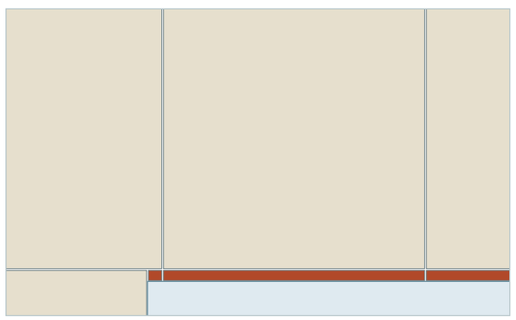

**NW-011: 61×47 мм / 1:28**

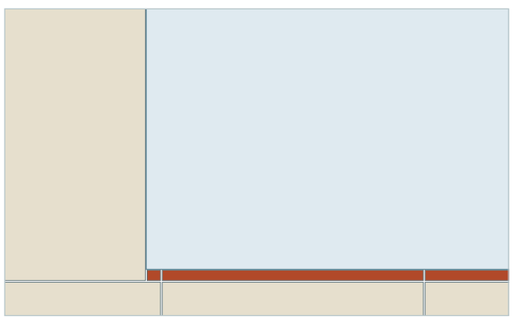

**NW-018: 1192×46 мм / 1:28**

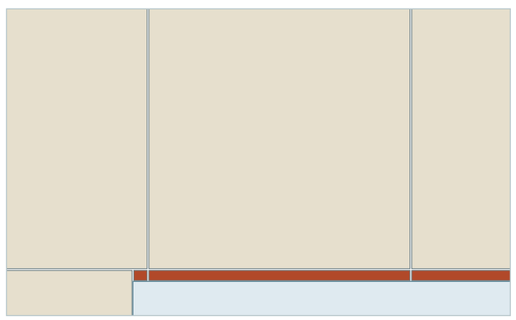

**33 × 1192 + 792 + 33 × 8 + 4 + 4 = 40400 мм**

437 деталей · 253.87 м²

Висота: 7 × 1250 + 661 + 7 × 8 + 4 + 4 = 9475 мм


Попереджень стіни: 61 · всі IDs у JSON

Номери у плитах: NW-NNN. Помаранчеві частини утримані від різання; перелік на арк.05.

# ПдЗх / торець

Плита 1192×1250 мм · шов 8 мм · справа 432 мм | 1:60, А3 без масштабування

Рядова сітка: 1250 + 8 = 1258 мм. Ряди не збігаються автоматично з поверхами.

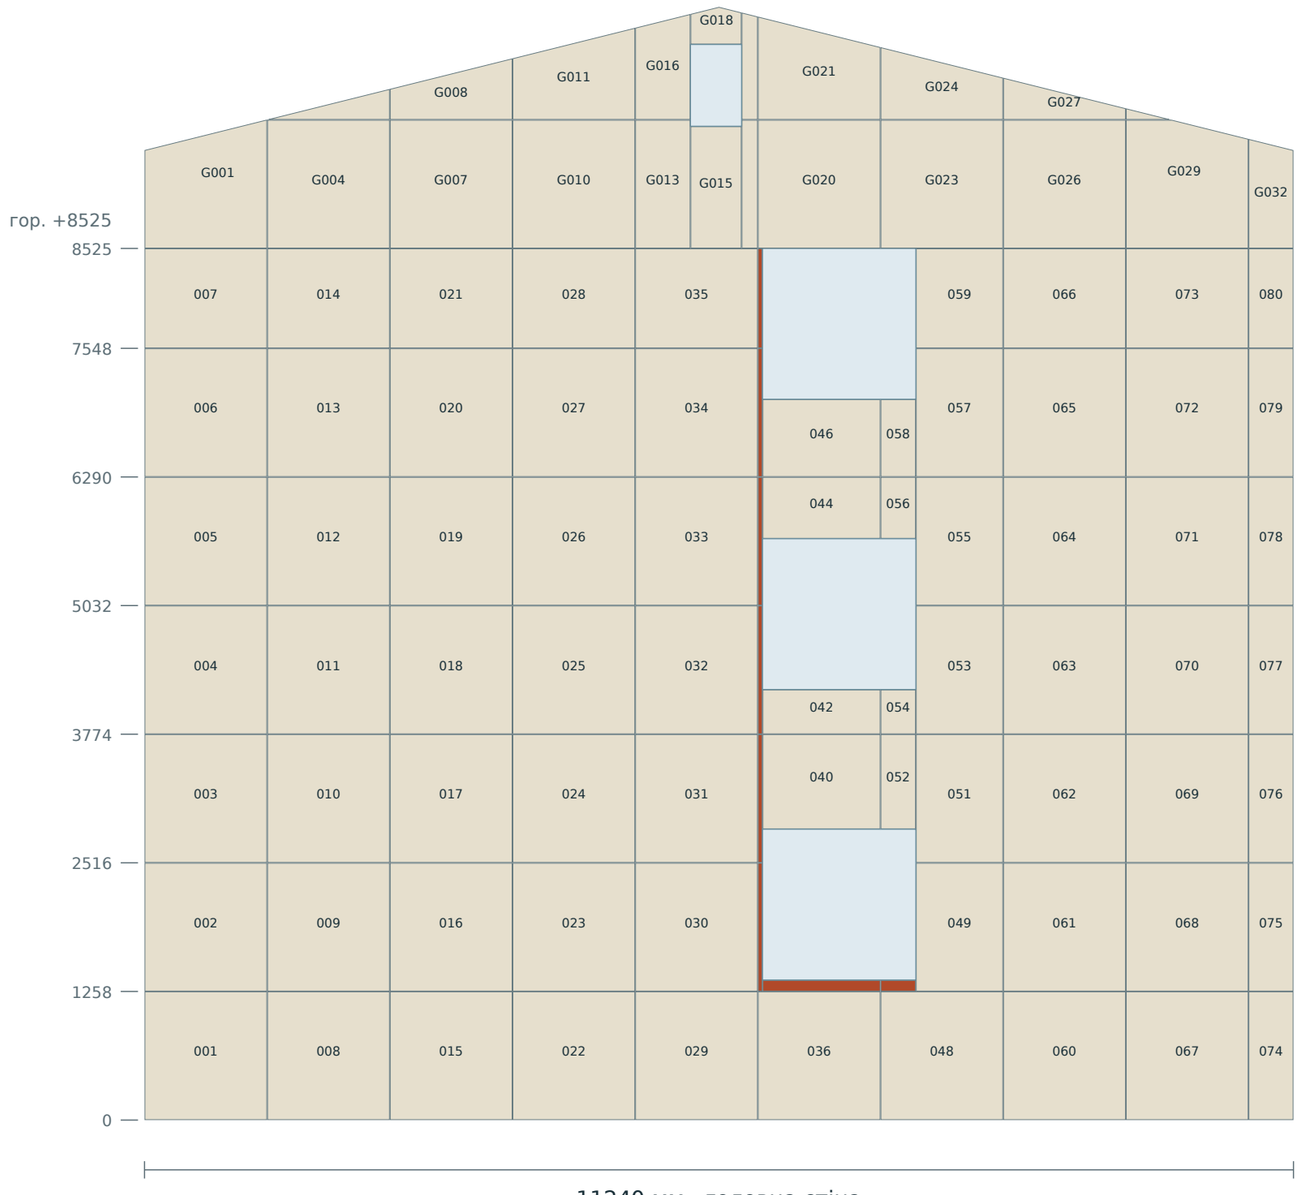


**1250 мм плита**

+ 8 мм шов

= 1258 мм ряд

**9 × 1192 + 432 + 9 × 8 + 4 + 4 = 11240 мм**

Висота: 6 × 1250 + 969 + 6 × 8 + 4 + 4 = 8525 мм

Номери у плитах: SW-NNN / SWG-NNN. Фронтон від +8525, скоси кандидатні.


102 деталей · 105.81 м²

Попереджень стіни: 8 · всі IDs у JSON

# ПнСх / торець

Плита 1192×1250 мм · шов 8 мм · справа 432 мм | 1:60, A3 без масштабування

Рядова сітка: 1250 + 8 = 1258 мм. Ряди не збігаються автоматично з поверхами.

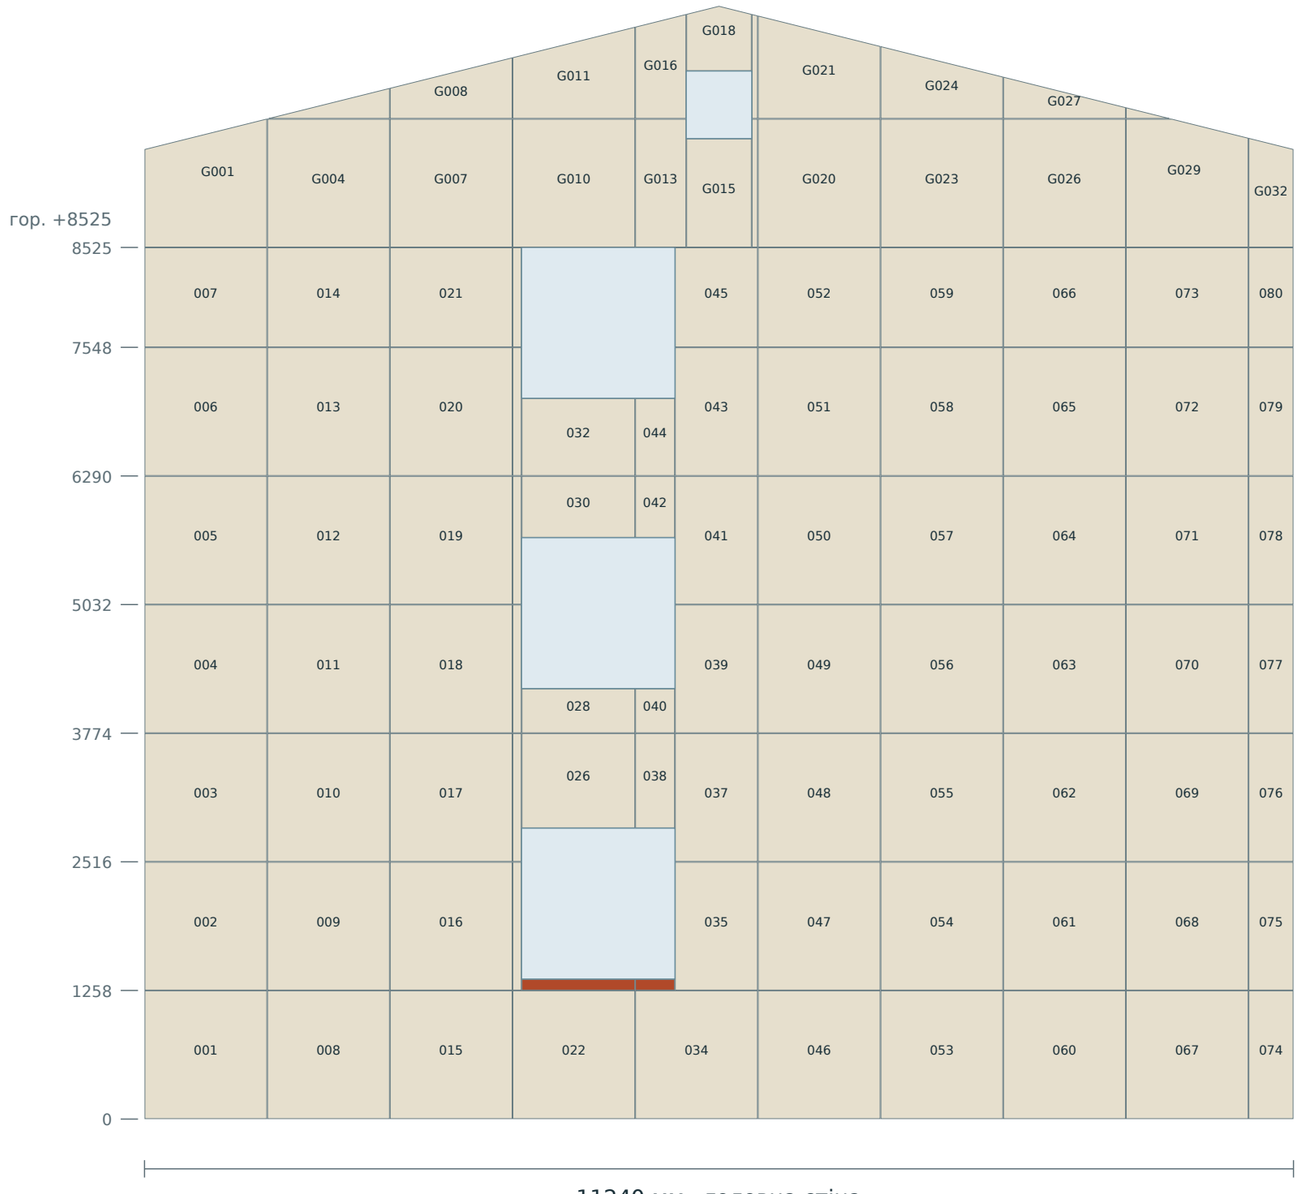


**1250 мм плита**

+ 8 мм шов

= 1258 мм ряд

**9 × 1192 + 432 + 9 × 8 + 4 + 4 = 11240 мм**

Висота: 6 × 1250 + 969 + 6 × 8 + 4 + 4 = 8525 мм

Номери у плитах: NE-NNN / NEG-NNN. Фронтон від +8525, скоси кандидатні.

102 деталей · 105.78 м²

Попереджень стіни: 2 · всі IDs у JSON

# Підсумок і утримані деталі

Чотири головні стіни + два фронтони. Це відомість геометрії; не закупівля й не допуск до різання.

## 1090 деталей = 1046 прямокутних + 44 профільованих

571 лист - евристичне пакування; не замовлення. Пропил 3 мм, крайове обрізання 0 мм - сценарій.

Чиста геометрична площа 768.38 м²; заготовки 771.19 м²; видалення скосами 2.81 м².

Нерозподілено 79.60 м² = залишки-кандидати 76.54 + прямокутний пропил 3.06; це не фактичні відходи.

| ФАСАД | ДЕТАЛЕЙ | ПЛОЩА, м² | ВУЗЬКІ / КОРОТКІ | ПРАВИЙ ЗАЛИШОК |
|---|---|---|---|---|
| SE / ПдСх / входи | 449 | 302.91 | 36 | 792 мм |
| NW / ПнЗх / балкони | 437 | 253.87 | 61 | 792 мм |
| SW / ПдЗх / торець | 80 | 87.84 | 8 | 432 мм |
| NE / ПнСх / торець | 80 | 87.84 | 2 | 432 мм |
| SWG / ПдЗх / фронтон | 22 | 17.96 | скоси: окрема звірка | 432 мм |
| NEG / ПнСх / фронтон | 22 | 17.94 | скоси: окрема звірка | 432 мм |

### 107 фасадних деталей з геометричними попередженнями - CSV для різання УТРИМАНО

ID / ширина×висота, мм. 50 мм ширини і 160 мм висоти - необхідні фільтри, не інженерне погодження.

| | | | |
|---|---|---|---|
| SE-003 277×103 | SE-347 32×1250 | NW-102 2×1250 | NW-301 1192×46 |
| SE-016 1192×103 | SE-350 392×42 | NW-111 371×46 | NW-303 1192×47 |
| SE-025 287×103 | SE-354 32×1250 | NW-123 851×46 | NW-314 372×46 |
| SE-048 392×74 | SE-357 32×1250 | NW-124 333×46 | NW-316 712×46 |
| SE-056 392×42 | SE-391 392×74 | NW-127 851×47 | NW-320 372×47 |
| SE-097 392×74 | SE-397 392×42 | NW-138 943×46 | NW-328 231×103 |
| SE-103 392×42 | SE-416 446×103 | NW-141 943×47 | NW-341 1192×103 |
| SE-122 809×103 | SE-429 1192×103 | NW-152 123×46 | NW-350 333×103 |
| SE-136 955×103 | SE-438 118×103 | NW-155 123×47 | NW-364 761×103 |
| SE-150 229×103 | NW-008 61×46 | NW-162 1192×46 | NW-378 1003×103 |
| SE-163 1192×103 | NW-011 61×47 | NW-164 1192×47 | NW-396 453×46 |
| SE-172 335×103 | NW-018 1192×46 | NW-172 471×46 | NW-408 933×46 |
| SE-193 22×1250 | NW-020 1192×47 | NW-173 712×46 | NW-409 251×46 |
| SE-195 392×74 | NW-028 533×46 | NW-176 471×47 | NW-412 933×47 |
| SE-200 22×1250 | NW-029 651×46 | NW-182 131×103 | NW-423 861×46 |
| SE-203 392×42 | NW-032 533×47 | NW-195 1192×103 | NW-426 861×47 |
| SE-207 22×1250 | NW-039 52×103 | NW-204 433×103 | SW-037 38×1250 |
| SE-210 22×1250 | NW-044 53×46 | NW-218 661×103 | SW-038 1146×104 |
| SE-244 392×74 | NW-056 1192×103 | NW-232 1103×103 | SW-039 38×1250 |
| SE-250 392×42 | NW-065 512×103 | NW-250 471×46 | SW-041 38×1250 |
| SE-269 826×103 | NW-079 582×103 | NW-262 951×46 | SW-043 38×1250 |
| SE-283 938×103 | NW-092 2×1250 | NW-263 233×46 | SW-045 38×1250 |
| SE-297 247×103 | NW-093 1182×103 | NW-266 951×47 | SW-047 38×969 |
| SE-310 1192×103 | NW-094 2×1250 | NW-277 843×46 | SW-050 338×104 |
| SE-319 317×103 | NW-096 2×1250 | NW-280 843×47 | NE-024 1103×104 |
| SE-340 32×1250 | NW-098 2×1250 | NW-291 222×46 | NE-036 381×104 |
| SE-342 392×74 | NW-100 2×1250 | NW-294 222×47 | |

44 профільовані деталі фронтонів: контур, опори, кріплення й операції довершення також залишаються кандидатами.

Джерело IDs: Mäe7-фасад-розкрій-v19.json. Без цоколя, відкосів, балконів, навісів і даху.

# Ціла заготовка з вирізом - тільки порівняння


Реальна комірка SE-GRID-C001-R003, проріз SE-W01. Не додається до кількостей чи native.

**Patina WOOD DIM rev02.2026, p17: рекомендує окремі секції біля прорізів.**

Гострі внутрішні кути, радіуси, кріплення й виробничий допуск цілого вирізу тут не погоджені.

## Поточний E: 2 секції

1250 мм / 1:10 · 4 мм до прорізу

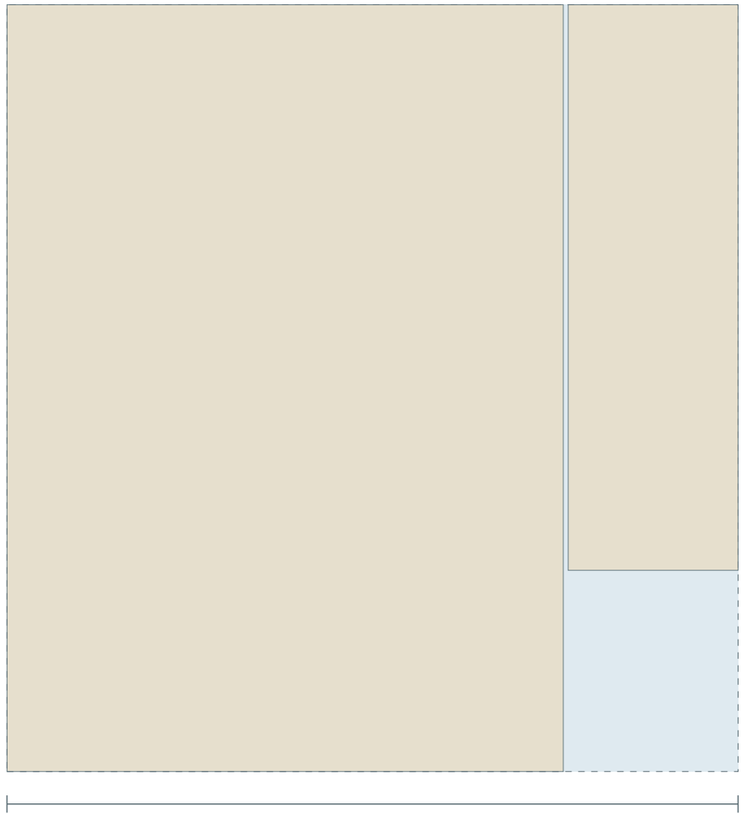


1192 мм · початкова готова плита

IDs: SE-004, SE-005

2 дет. / 1.38914 м² збереженої геометрії

## Порівняння: одна Г-подібна деталь

1250 мм / 1:10 · 4 мм до прорізу

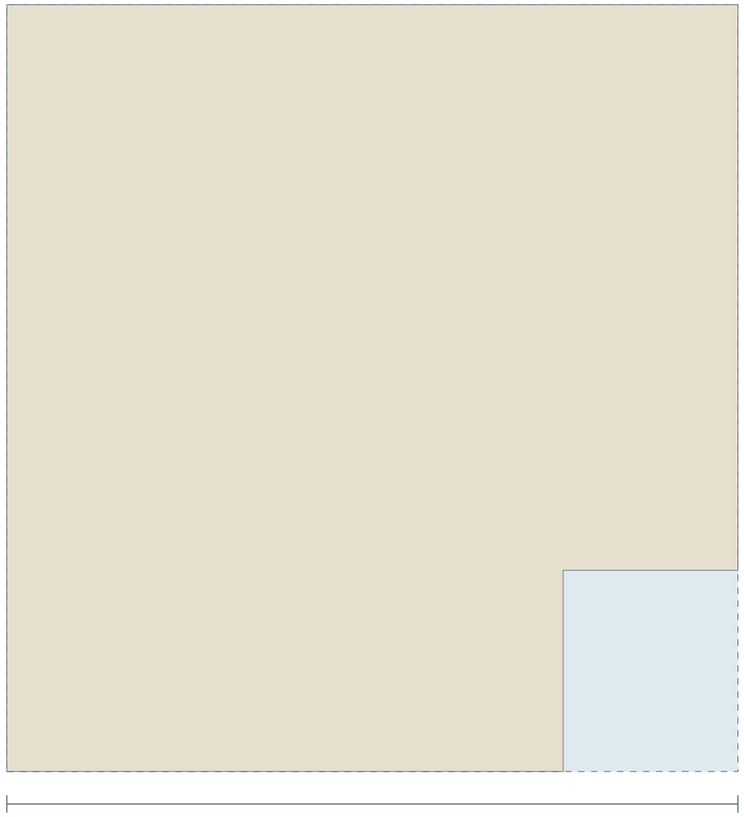

1192 мм · початкова готова плита

IDs: SE-GRID-C001-R003-C01

1 дет. / 1.39652 м² збереженої геометрії

Пунктир - початкова заготовка. Блакитне - вилучений матеріал. Праворуч немає зайвого шва між секціями.

Різниця площі виникає від шва між прямокутними секціями; це не доказ економії, міцності чи придатності вирізу.
APPROVED=false · READY TO CUT=false · порівняльні IDs не замінюють відомість 1090 деталей.