
ПдСх · входи

Поточні контури тих самих плит моделі: 318 на стіні. Плита1192×1250 / шов8 мм; цілий лист із зарізом — порівняльний варіант.

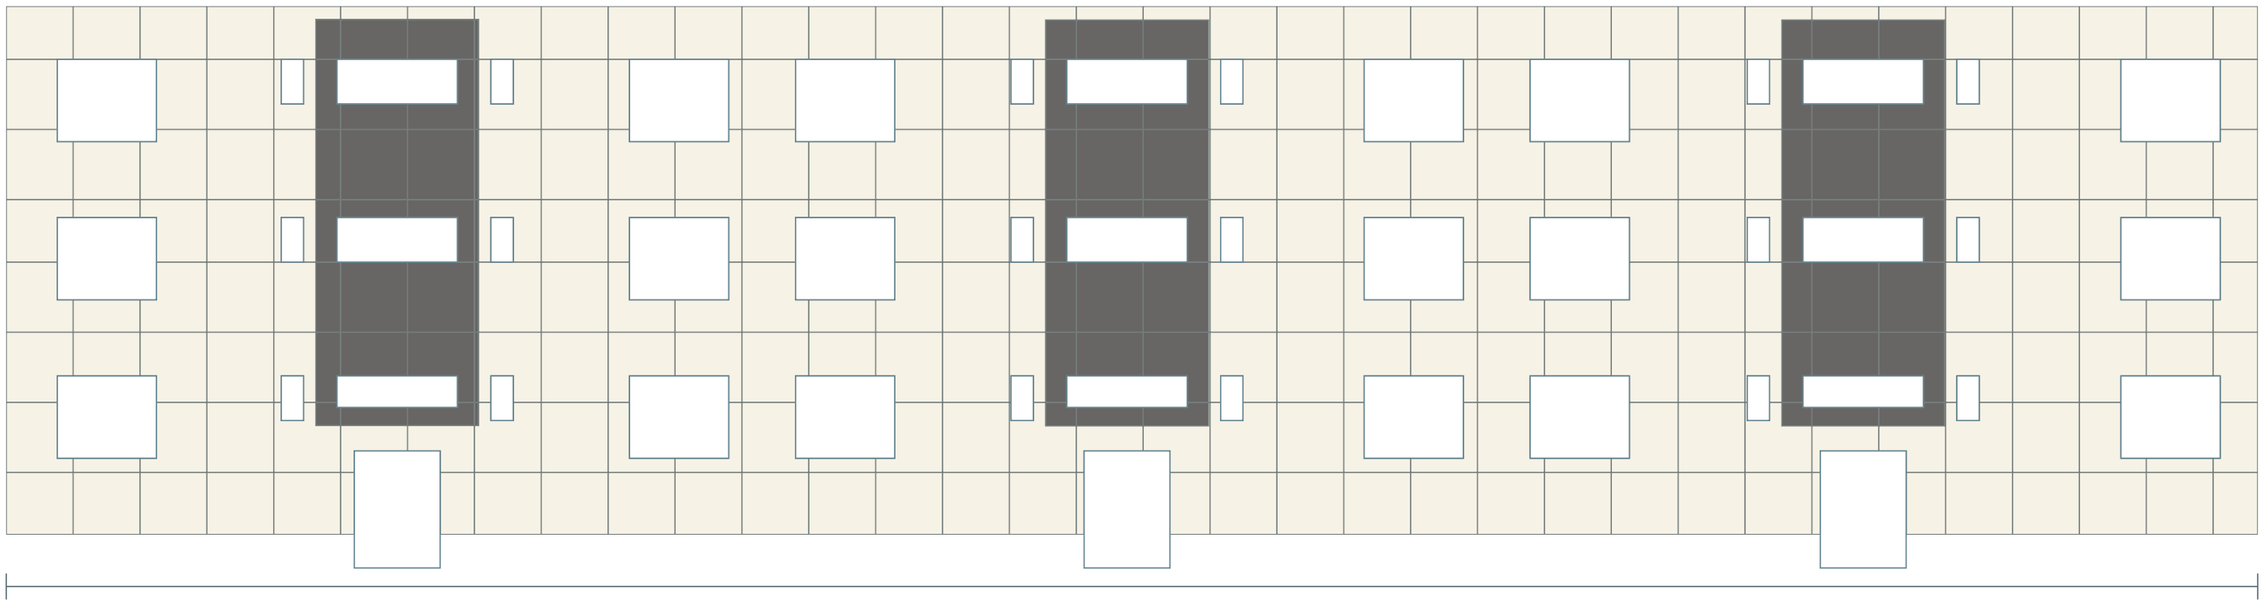

40400 мм · графічна геометрія; обмір не виконаний


P222 / P070 — за легендою арк05/06. Положення A05 звірено з PDF53.

Отвори й контури — спільні з моделлю. На NW сірі межі виступів не є новими віконними отворами.

Сітка9 точок, парні дошки100×25, стрічка100: кандидат; крайові опори й кріплення ще погоджуються.

ПнЗх · балкони

Поточні контури тих самих плит моделі: 291 на стіні. Плита1192×1250 / шов8 мм; цілий лист із зарізом — порівняльний варіант.

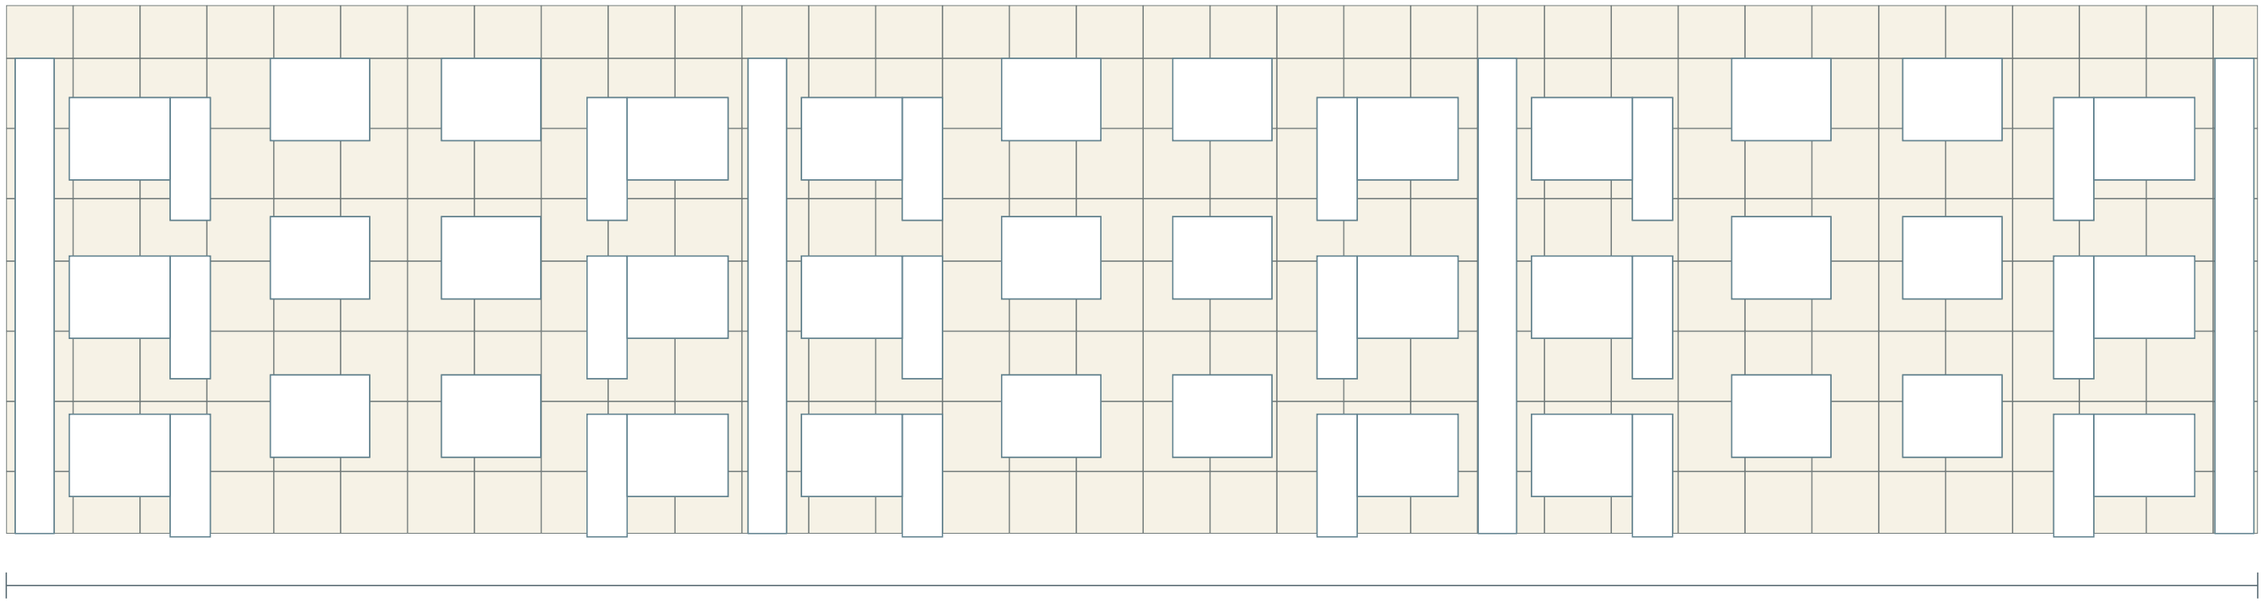

40400 мм · графічна геометрія; обмір не виконаний


P222 / P070 — за легендою арк05/06. Положення A05 звірено з PDF53.

Отвори й контури — спільні з моделлю. На NW сірі межі виступів не є новими віконними отворами.

Сітка9 точок, парні дошки100×25, стрічка100: кандидат; крайові опори й кріплення ще погоджуються.

ПдЗх · торець

Поточні контури тих самих плит моделі: 70 на стіні + 18 фронтону. Плита1192×1250 / шов8 мм; цілий лист із зарізом — порівняльний варіант.

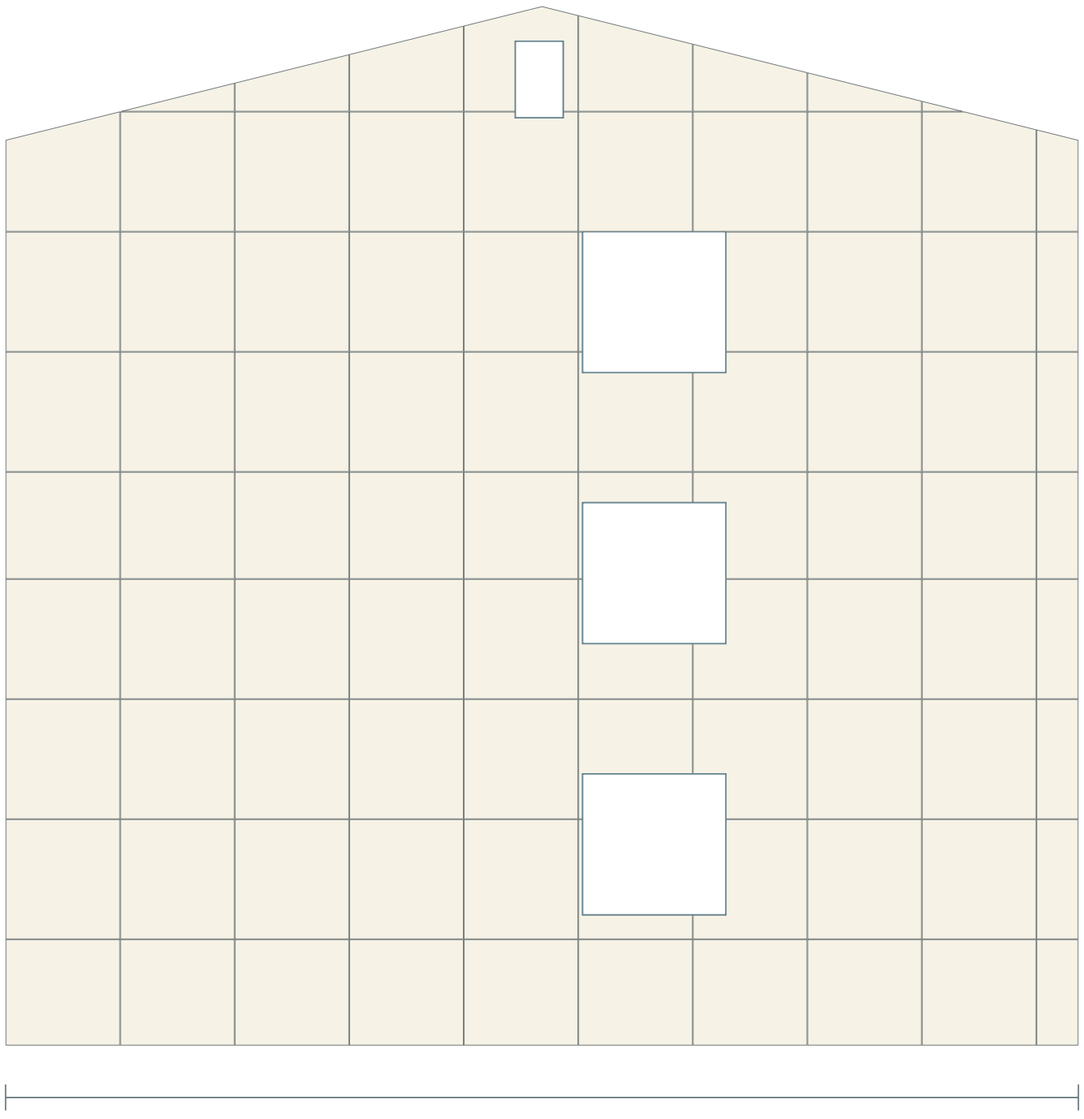

11240 мм · графічна геометрія; обмір не виконаний


P222 / P070 — за легендою арк05/06. Положення A05 звірено з PDF53.

Отвори й контури — спільні з моделлю. На NW сірі межі виступів не є новими віконними отворами.

Сітка9 точок, парні дошки100×25, стрічка100: кандидат; крайові опори й кріплення ще погоджуються.

ПнСх · торець

Поточні контури тих самих плит моделі: 70 на стіні + 18 фронтону. Плита1192×1250 / шов8 мм; цілий лист із зарізом — порівняльний варіант.

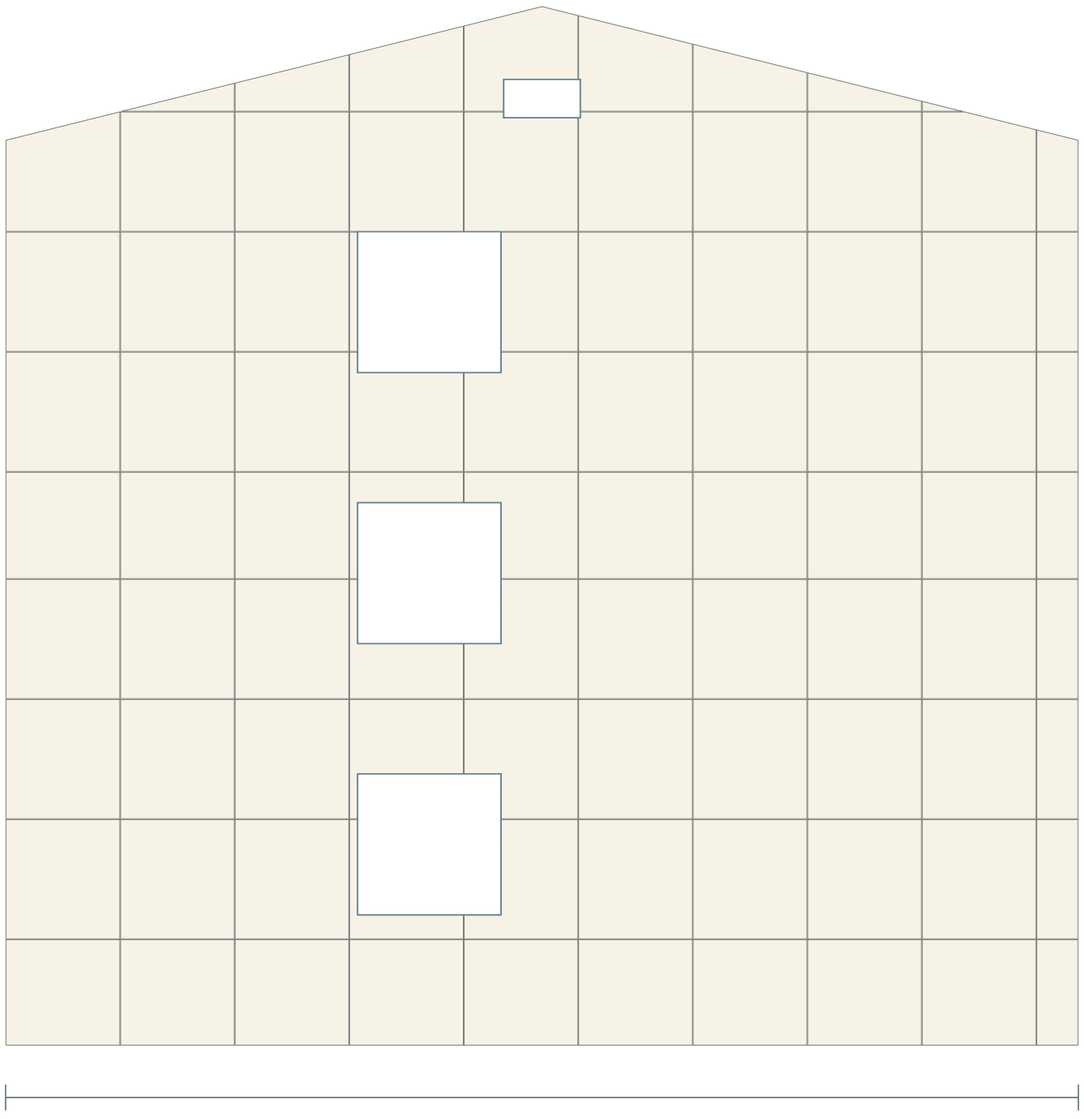

11240 мм · графічна геометрія; обмір не виконаний


P222 / P070 — за легендою арк05/06. Положення A05 звірено з PDF53.

Отвори й контури — спільні з моделлю. На NW сірі межі виступів не є новими віконними отворами.

Сітка9 точок, парні дошки100×25, стрічка100: кандидат; крайові опори й кріплення ще погоджуються.

Ділянка · контури з аркуша01 / PDF49

Координати графічно прив’язані до будинку40,4×11,24 м; межі штрихування місцями інтерпольовані. Це не топозйомка.

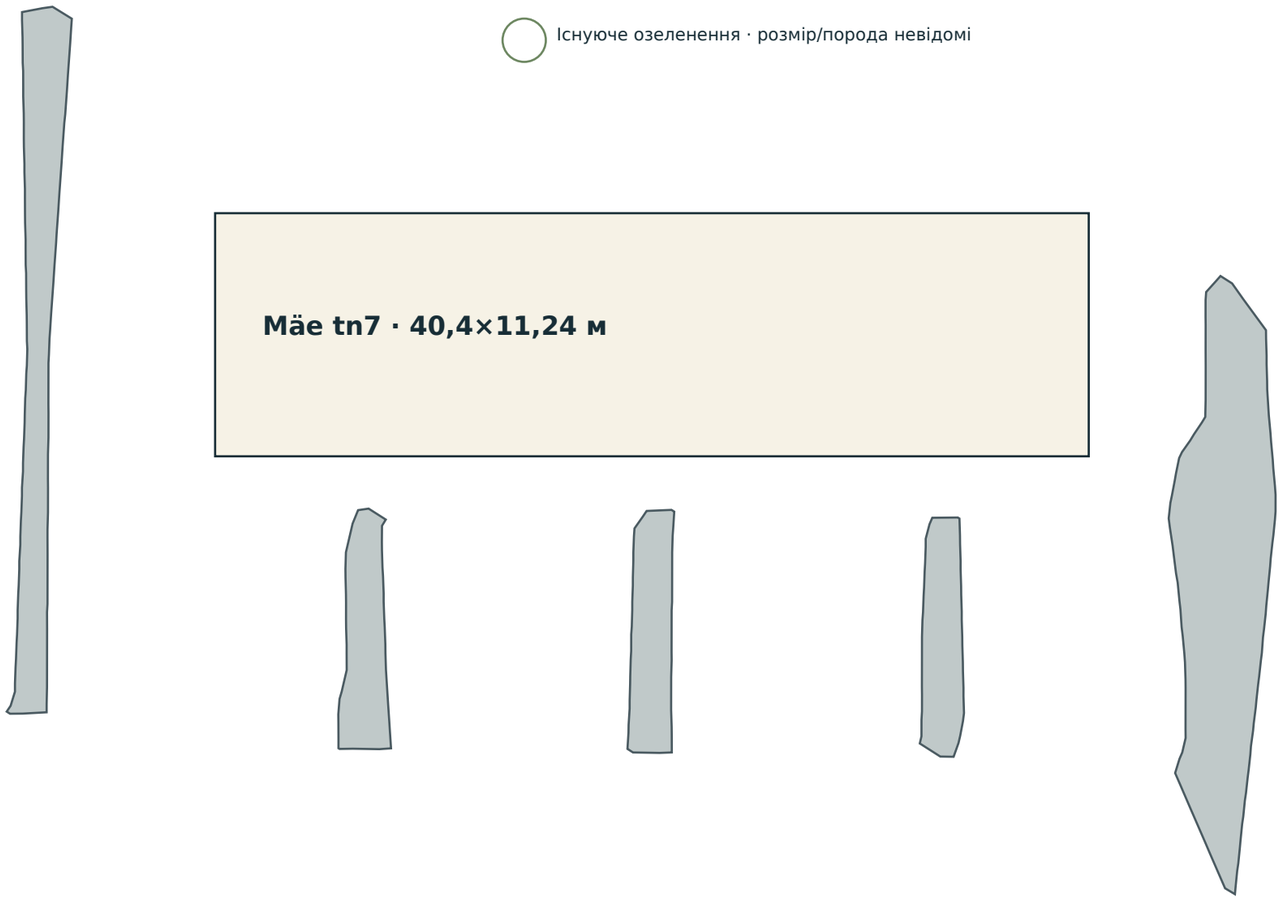

Проєктний обсяг асфальту: 200 м². Обчислена площа показових контурів: 198.138 м².

Різниця не прихована масштабуванням. Ухили, висоти рельєфу, точні межі й кількість дерев потребують обміру.

П’ять окремих зон покриття та графічна прив’язка озеленення; у закупівлю вони не включені.

Матеріали · джерело і вигляд

Код, тип і розміри — з проєкту; оптичні параметри — для огляду. Постачальник, замовлений продукт і поставлена партія невідомі.

Елемент	Параметри	Вигляд у моделі	Що ще уточнити
Покрівельний метал PDF: 19, 53, 60	Classic / PURAL / RR23 · 0.6 мм. 32/475 мм — лише довідковий профіль Ruukki EE	Цифровий зразок RR23 виробника; блиск, шорсткість і відбиття — кандидат	Виробник, модель замка, партія покриття, радіуси та кріплення
Підпокрівельна мембрана PDF: 19, 60	Код не задано · товщина за вузлом мм. Контррейка32×50; обрешітка32×100 мм	Показова темна поверхня; 0,2 мм — товщина для відображення	Продукт, товщина, нахльости та сумісність
Деревина підконструкцій PDF: 19, 21, 57	H3; для софіту Bs1,d0 · товщина за вузлом мм. Фасад50×50 і25×100; дах32×50 і32×100; цоколь50×75; софіт22×100 мм	Показова деревна фактура; порода й колір партії невідомі	Порода, сорт міцності, засіб просочення, вогнезахисна партія; існуючі крокви
Фіброцементні плити PDF: 21, 53	P222 / P070 · 8 мм.	Цифрові зразки сучасного виробника; не обмір поставленої партії	Замовлений продукт і покоління, партія, погоджений фізичний зразок
Фасадна мінеральна вата PDF: 21, 29	λ≤0,035 Вт/(м·K) · 200 мм. 100+50+50 мм; не менше200 мм	Показові волокна; колір і густина цифрової поверхні не сертифікують продукт	Виробник, продукт, густина й партія
Утеплення горищного перекриття PDF: 19, 20, 29, 60	PP-1; λ≤0,041; клас A · 450 мм. Старі250 мм видаляються; утеплюється горизонтальне перекриття	Показовий волокнистий шар; не утеплення всіх схилів	Продукт, монтажна густина, осідання й партія
Вітрозахисна гіпсова плита PDF: 21, 56	Код не задано · 9 мм. Проклеєні стики	Показова поверхня; сучасний Gyproc GTS9 має9,5 мм і не є точною підміною	Виробник, тип плити та сумісна стрічка
Захисна стрічка під фіброцементом PDF: 21	Код не задано · товщина за вузлом мм. 100 мм ширина і2 мм товщина — цифровий кандидат, не проєктні розміри	Показова чорна гума; збільшення90→100 не погоджує вузол парних дощок	Система, профіль ребер, ширина, товщина, стики та сумісність
Відливи й металеві обрамлення PDF: 23, 53	PURAL / RR23 · 0.6 мм. Винос30 мм; біля балконів10 мм; нахил≥1:10	Цифровий RR23; блиск і згини — кандидати	Профілі згинів, покриття, герметики, кути та кріплення

Матеріали · джерело і вигляд

Код, тип і розміри — з проєкту; оптичні параметри — для огляду. Постачальник, замовлений продукт і поставлена партія невідомі.

Елемент	Параметри	Вигляд у моделі	Що ще уточнити
Нові вікна PVC і склопакети PDF: 23, 73, 74	PVC; прозоре потрійне скління; керамічна дистанційна рамка · товщина за вузлом мм. Темно-сірі зовні, білі всередині; U≤0,9/1,1 за типом	Колірна сім’я за проєктом; RGB, IOR, transmission і шорсткість — кандидати	Профіль постачальника, склад скла, газ, покриття, крайове ущільнення та точний колір
Вхідні двері PDF: 24, 53, 75	VU01; утеплений алюміній / RR23; прозоре загартоване скло · товщина за вузлом мм. U≤1,4; скло12 мм у моделі — лише кандидат	Цифровий RR23 і показова оптика; не замовлений IGU	Терморозрив, переріз профілю, склад і товщина скла, оптичні покриття
Покриття даху тамбура PDF: 25, 53, 68	SBS ↔ Classic / PURAL · товщина за вузлом мм. Для вузла Classic лист0,6 мм;32×50 і32×100 мм	Візуалізований Classic — вибір вузла, не погоджене усунення суперечності	Підтвердження проєктанта щодо застосовного вузла й продукту
Сталь балконів PDF: 26, 53	S355JR / C3 / RR23 · товщина за вузлом мм. 100×100×5;100×50×5;50×50×5;L50×50×5; огорожа40×40×3 і40×80×3 мм	Цифровий RR23; фактура фарби й гострі кути — кандидати	Система фарбування, адгезія, радіуси, анкери та зварювання
Сталь козирка входу PDF: 25	S355JR / C3 / гаряче цинкування · товщина за вузлом мм. RHS100×80×5 мм	Показове цинкування; реальний візерунок і старіння невідомі	Ванна й товщина покриття, отвори, зварювання та кріплення
Балконне скло PDF: 26	Прозоре загартоване; верхнє сіре загартоване ламіноване · [6] мм. Верхнє4+4 мм; міжшар невідомий	IOR, пропускання, тон і відбиття — цифрові кандидати	Виробник системи, міжшар, VLT, тонування, край і напрямні
Підлога балкона PDF: 26, 65	Цементно-стружкова плита; неслизький PU або аналог · 24 мм. Гума1,5×50; PURAL0,6 мм; ухил≥1:80; примикання≥100 мм	Показова поверхня;1 мм фінішу й порядок шарів — кандидати	Плита, покриття, товщина фінішу, клас ковзання, гума й робочий водний вузол
Цокольне утеплення й профілі PDF: 18, 28, 57	EPS; приклад EPS120 Perimeeter; MP25/38 або аналог · 150 мм. 100+50 мм; λ≤0,035;120 кПа; дерево50×75; профіль25 мм; FC8 P070	Показова структура EPS та цинку; колір FC — цифровий зразок	EPS продукт і партія, калібр/переріз hat, гідроізоляція й анкери
Збережені підвальні вікна PDF: 23, 63	Код не задано · товщина за вузлом мм. Нові відливи0,6 PURAL; вузол дерево75×30; RKL31 30 мм або аналог	Біла рама і прозора площина — лише оптична репрезентація існуючого	Обмір, існуючі рама/скло, посадка, відкоси та прив’язка вузла

Матеріали · джерело і вигляд

Код, тип і розміри — з проєкту; оптичні параметри — для огляду. Постачальник, замовлений продукт і поставлена партія невідомі.

Елемент	Параметри	Вигляд у моделі	Що ще уточнити
Кріплення та кронштейни PDF: 21, 57	C3; цинк≥275 г/м² для кронштейнів/hat · товщина за вузлом мм. L150×150×60×2,5 мм; не менше5 випробувань витягування	Показові металеві поверхні;9 маркерів не є просвердленими отворами чи специфікацією	Вироби, діаметри, стіна, крайові відстані, навантаження та погодження
Бетонне вимощення PDF: 18	C30/37 / XC4+XF3 / B500 · товщина за вузлом мм. Ширина600 мм; ухил≥2%; щебінь200 мм0–32; сіткаØ6@150×150 мм	Показова бетонна поверхня; не скан фактичної суміші	Товщина, рівні, положення арматури й контакт з фундаментом