

ПдСх / входи

Зліва 1200 мм → шов 8 мм → справа 528 мм | 1:125 при друці А3 без масштабування

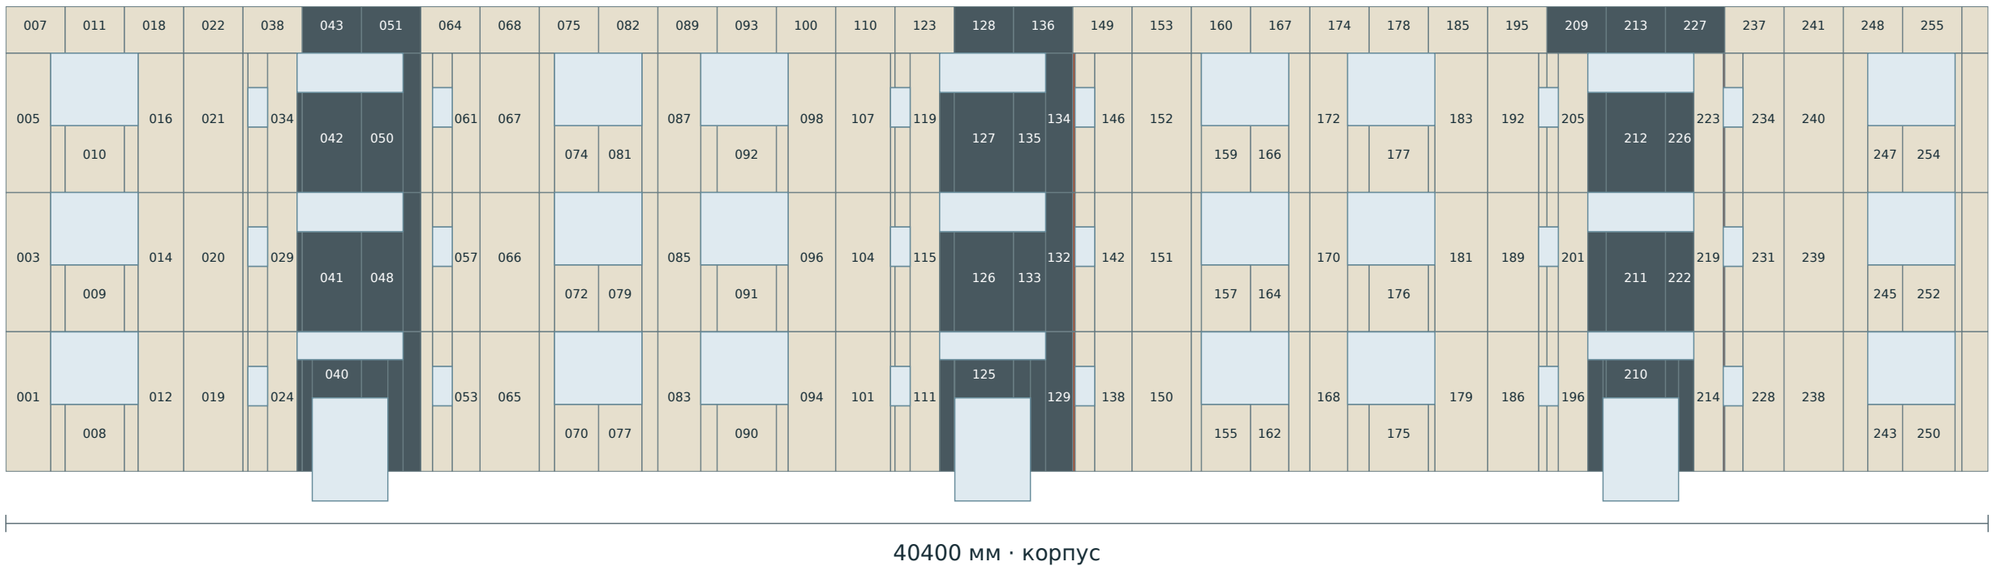


40400 мм · корпус


SE-124 / 5 мм / 1:30

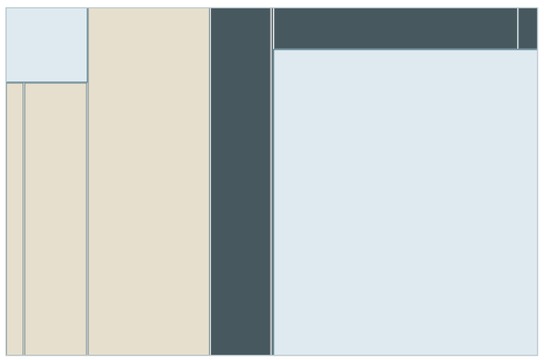

SE-137 / 39 мм / 1:30

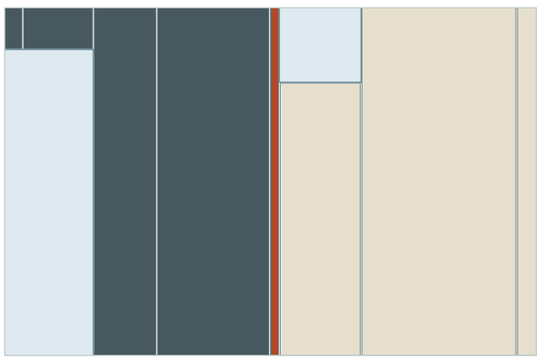

SE-215 / 22 мм / 1:30

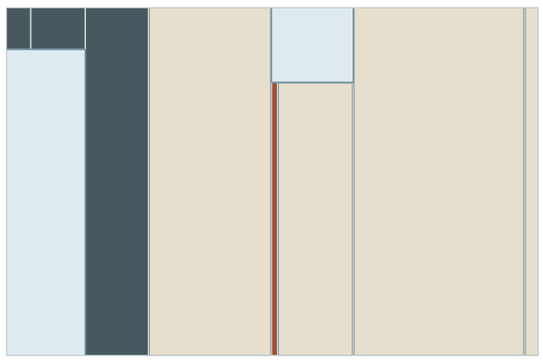


33 × 1200 + 528 + 33 × 8 + 4 + 4 = 40400 мм

259 деталей · 303.58 м²


Помаранчеві вузькі деталі: 10. Їх не передавати на різання; див. аркуш 05.

ПнЗх / балкони


Зліва 1200 мм → шов 8 мм → справа 528 мм | 1:125 при друці А3 без масштабування

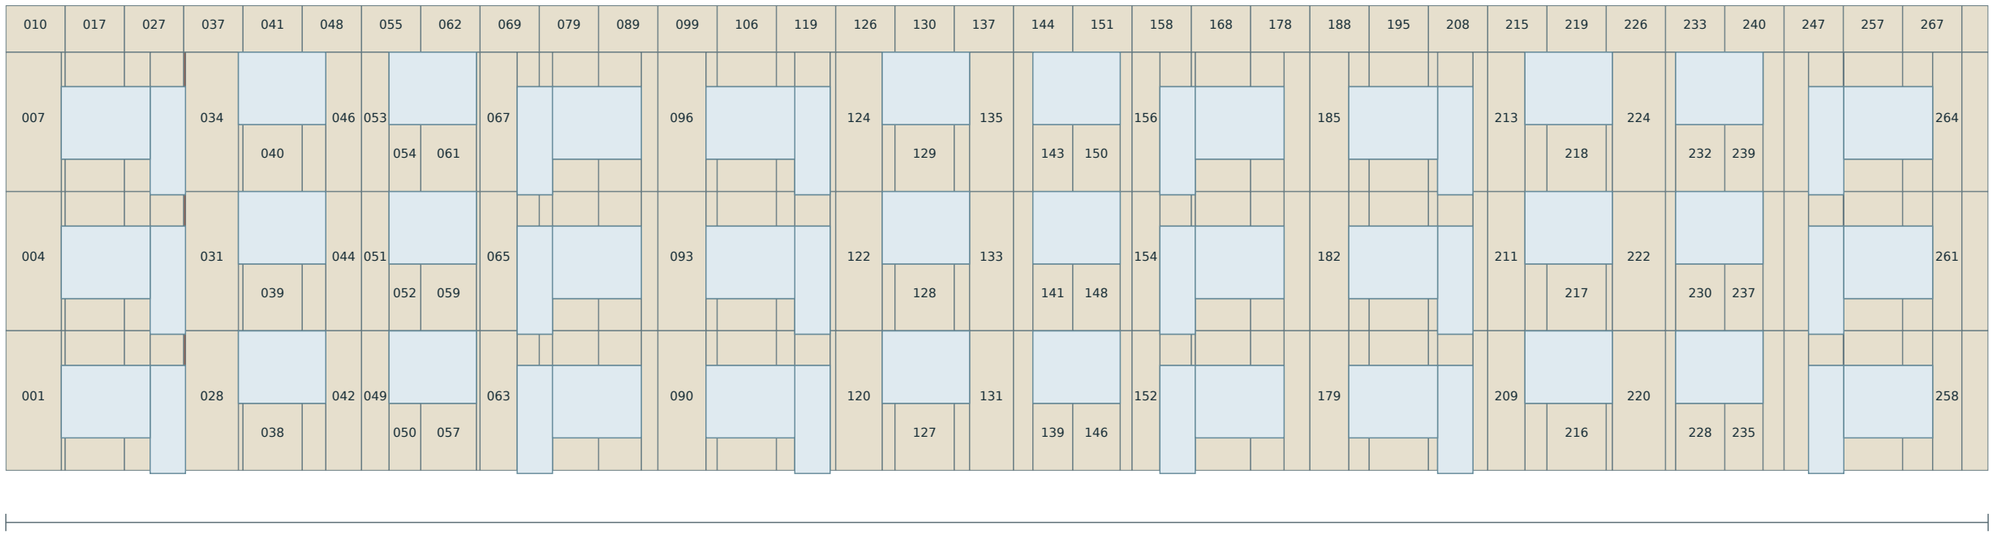

NW-029 / 29 мм / 1:30

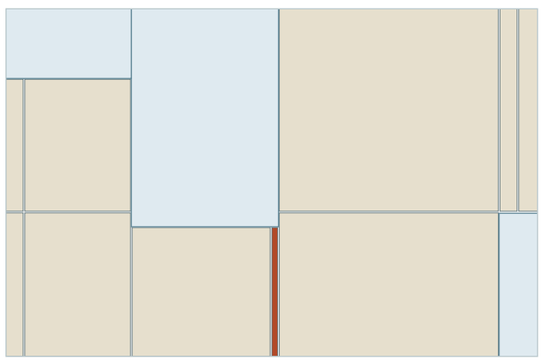

NW-250 / 3 мм / 1:30

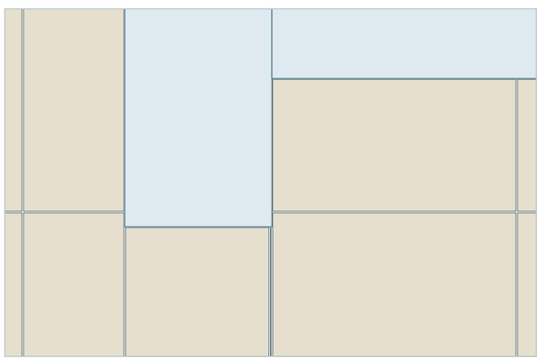


33 × 1200 + 528 + 33 × 8 + 4 + 4 = 40400 мм

271 деталей · 254.56 м²

Помаранчеві вузькі деталі: 6. Їх не передавати на різання; див. аркуш 05.

ПдЗх / торець

Зліва 1200 мм → шов 8 мм → справа 360 мм | 1:60 при друці А3 без масштабування

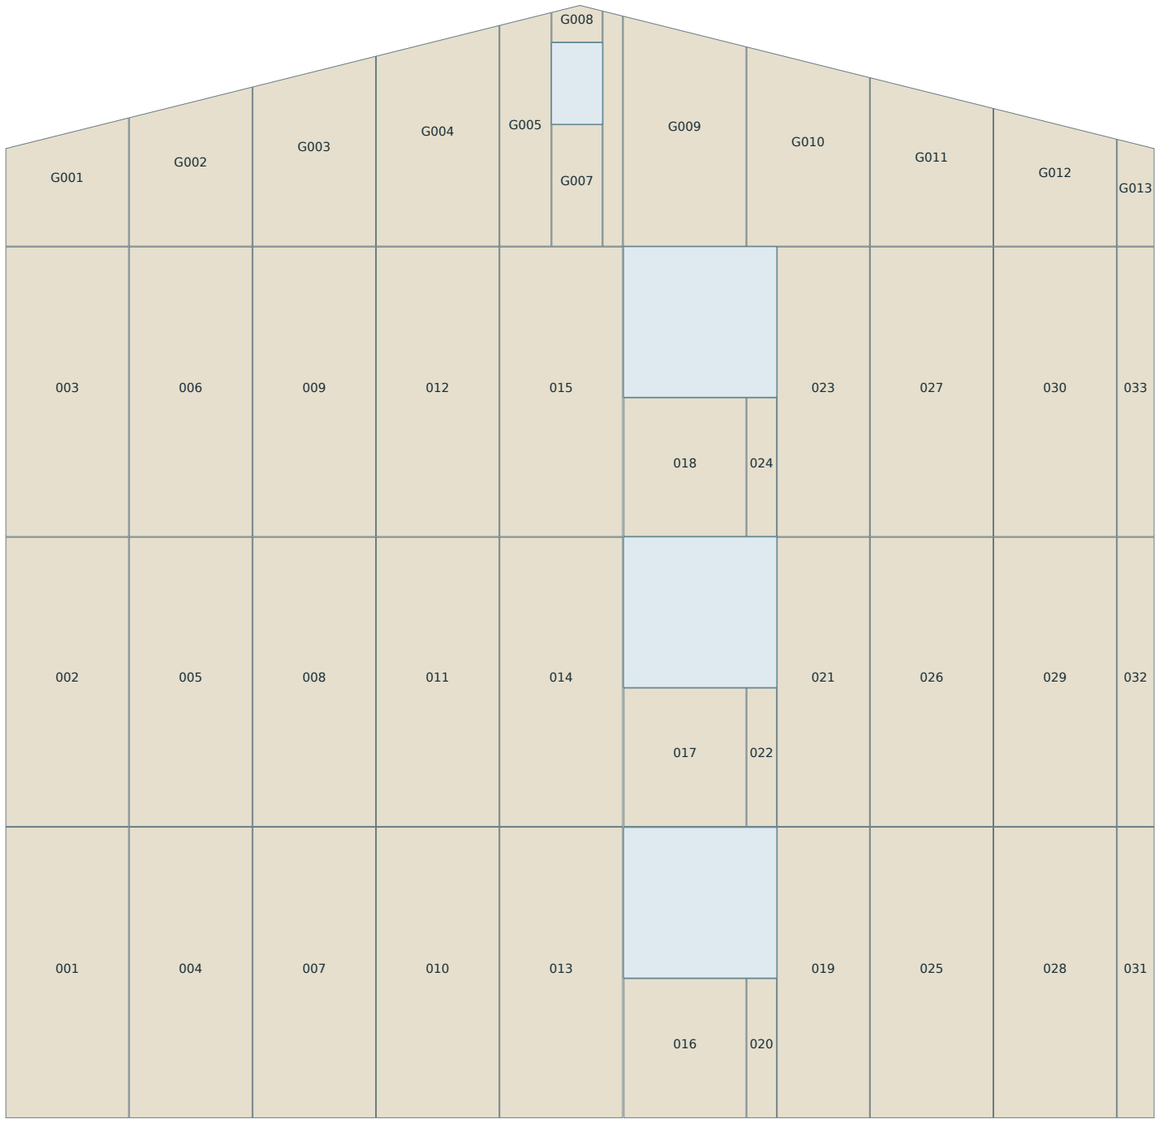


9 × 1200 + 360 + 9 × 8 + 4 + 4 = 11240 мм

46 деталей · 106.21 м²

Торець і фронтон мають спільну сітку. Скоси, опори й кріплення потребують звірки.

ПнСх / торець

Зліва 1200 мм → шов 8 мм → справа 360 мм | 1:60 при друці А3 без масштабування

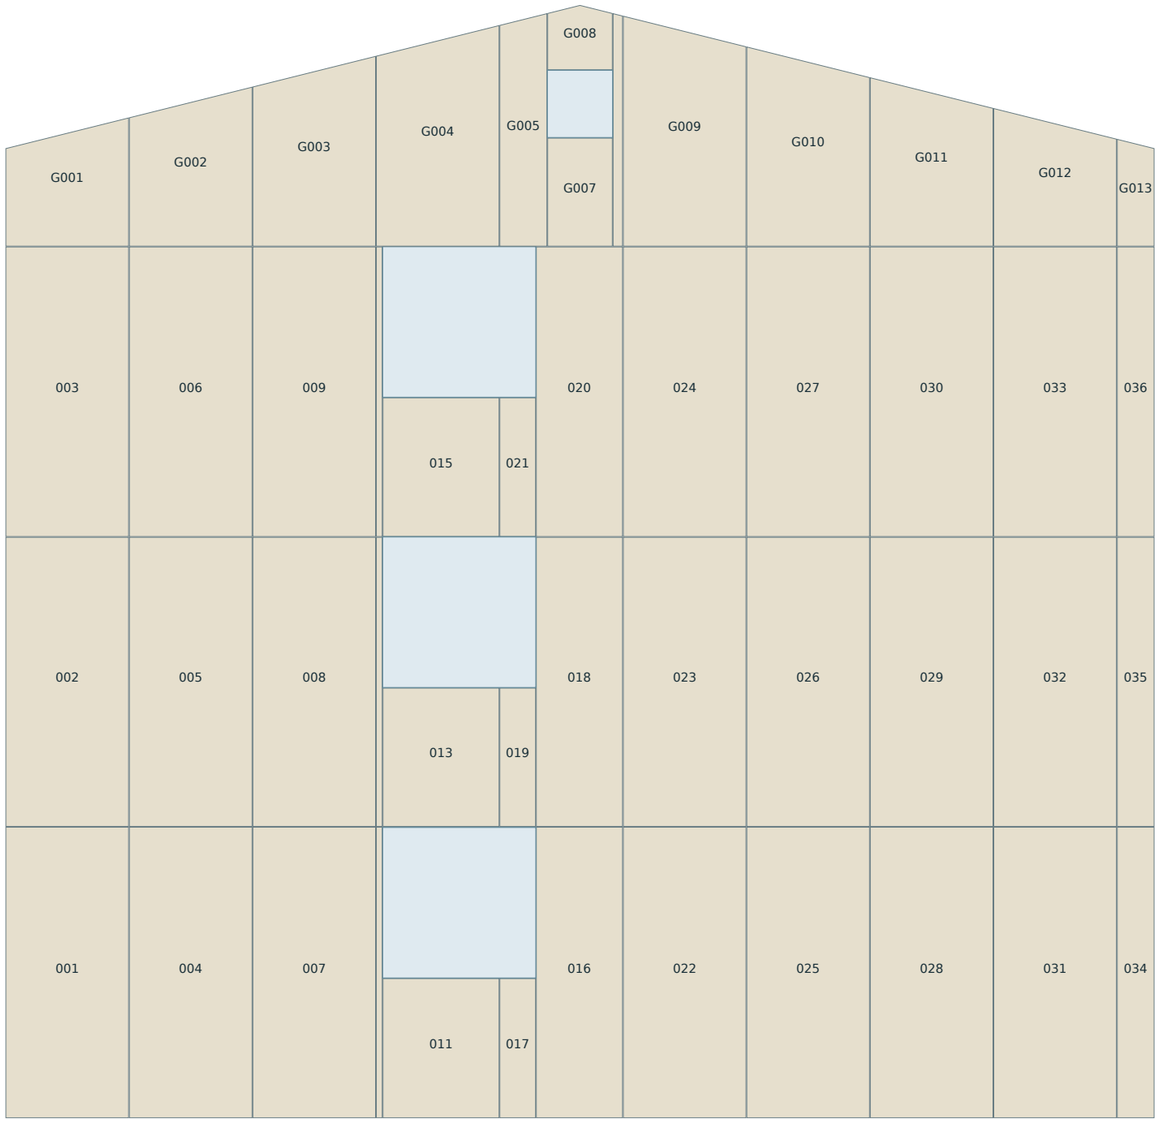

9 × 1200 + 360 + 9 × 8 + 4 + 4 = 11240 мм

11240 мм · корпус

49 деталей · 106.17 м²

Торець і фронтон мають спільну сітку. Скоси, опори й кріплення потребують звірки.

Вузькі ділянки біля прорізів

Сітка 1208:0 збережена. Локальне рішення потрібне до різання; всю стіну довільно не зсуваємо.

ДЕТАЛЬ	ШИРИНА × ВИСОТА, мм	X / Y, мм зліва знизу
SE-124	5 × 2272	19332 / 4
SE-137	39 × 2842	21748 / 4
SE-141	39 × 2827	21748 / 2854
SE-145	39 × 2832	21748 / 5689
SE-215	22 × 1332	35006 / 4
SE-216	22 × 702	35006 / 2144
SE-220	22 × 1324	35006 / 2854
SE-221	22 × 695	35006 / 4986
SE-224	22 × 1327	35006 / 5689
SE-225	22 × 697	35006 / 7824
NW-029	29 × 630	3628 / 2144
NW-032	29 × 634	3628 / 4982
NW-035	29 × 697	3628 / 7824
NW-250	3 × 630	37452 / 2144
NW-253	3 × 634	37452 / 4982
NW-256	3 × 697	37452 / 7824

16 конфліктів / 3-39 мм

Вікна залишені за джерелом.

Сітка й правий залишок збережені.

Різання цих смужок заблоковане.

Локальне рішення: деталь примикання,

поділ або погоджена зміна біля вікна.

50 мм тут лише необхідний фільтр крайових відстаней, не розрахунок.

Загальний розкрій: 625 деталей.

1200 × 3050 мм - сценарій листа.

Формат / запас краю / пропил

звірити з етикеткою й інструментом.

Джерело геометрії: Mäe7-фасад-розкрій-v18.json · спільні IDs моделі та відомості.