
ПдСх / входи

Плита 1192×1250 мм · шов 8 мм · справа 792 мм | 1:125, А3 без масштабування


Рядова сітка: 1250 + 8 = 1258 мм. Ряди не збігаються автоматично з поверхами.

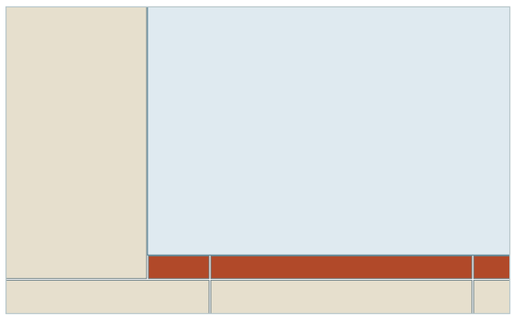


SE-003: 277×103 мм / 1:28



SE-016: 1192×103 мм / 1:28

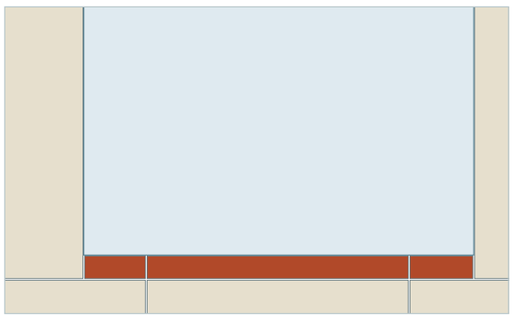

SE-025: 287×103 мм / 1:28

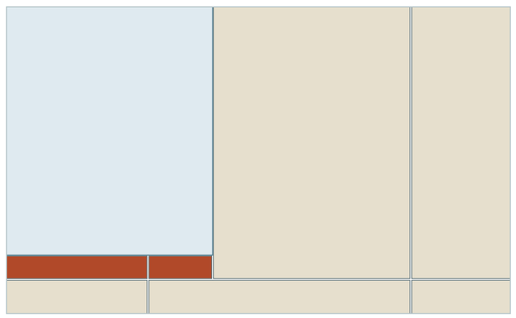

33 × 1192 + 792 + 33 × 8 + 4 + 4 = 40400 мм

449 деталей · 302.91 м²

Висота: 7 × 1250 + 661 + 7 × 8 + 4 + 4 = 9475 мм


Попереджень стіни: 36 · всі IDs у JSON

Номери у плитах: SE-NNN. Помаранчеві частини утримані від різання; перелік на арк.05.

ПнЗх / балкони


Плита 1192×1250 мм · шов 8 мм · справа 792 мм | 1:125, А3 без масштабування

Рядова сітка: 1250 + 8 = 1258 мм. Ряди не збігаються автоматично з поверхами.

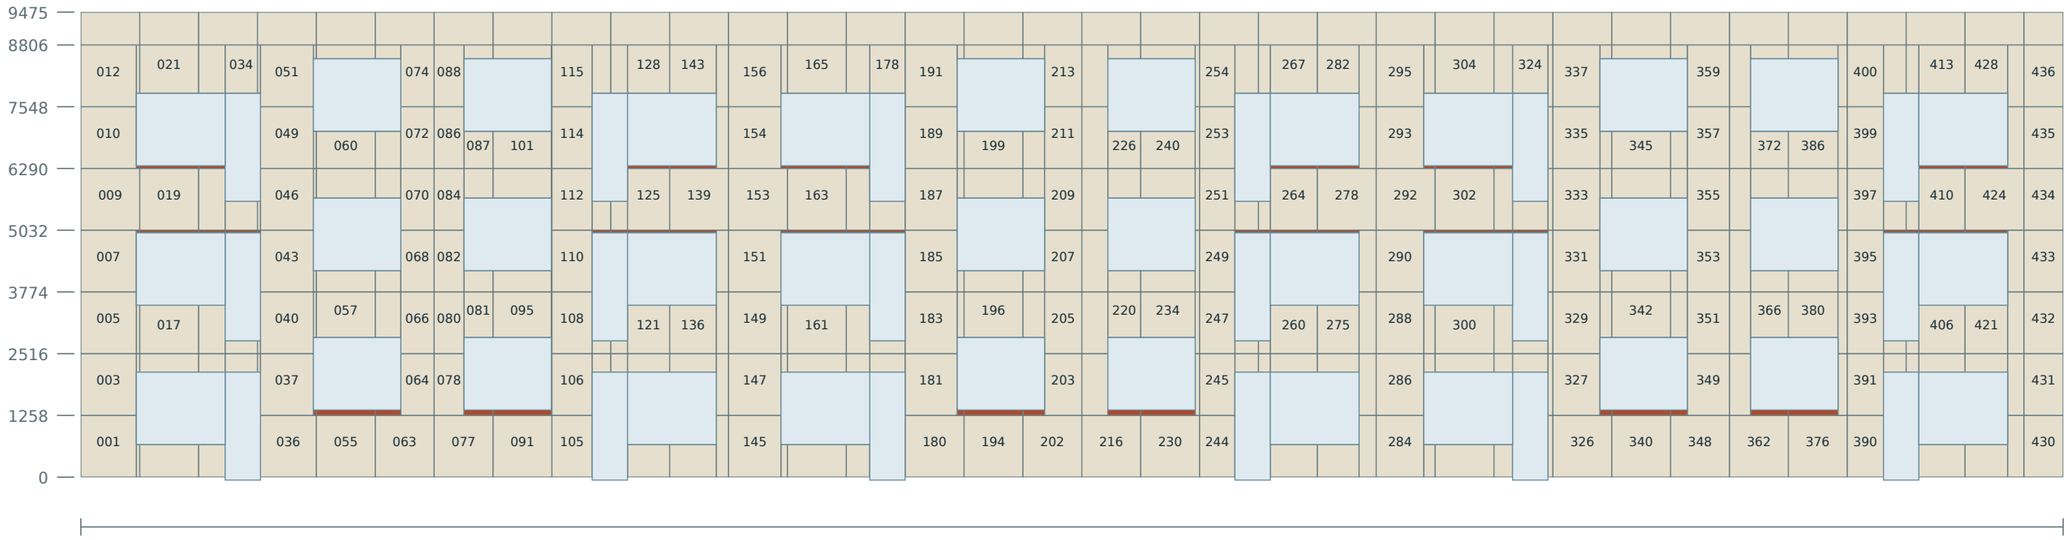


40400 мм · головна стіна


NW-008: 61×46 мм / 1:28

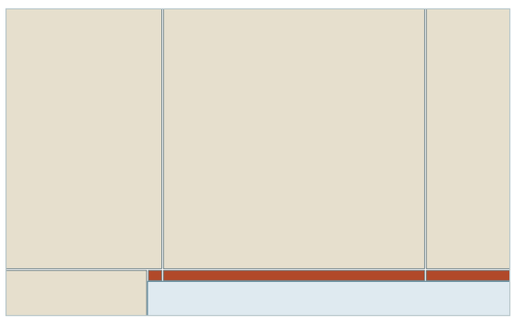

NW-011: 61×47 мм / 1:28

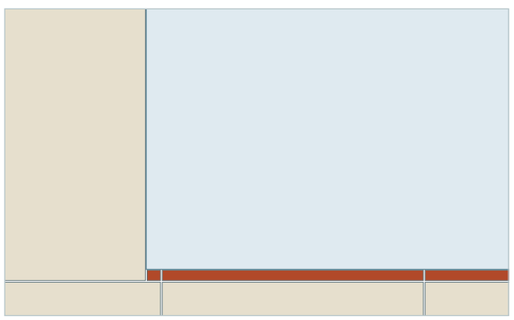

NW-018: 1192×46 мм / 1:28

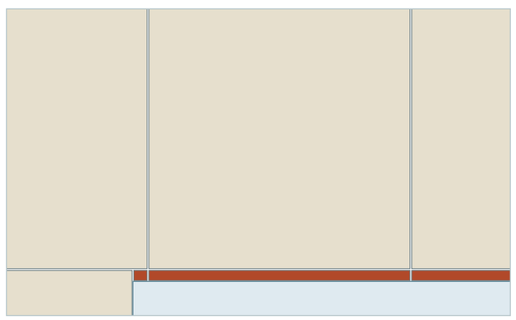

33 × 1192 + 792 + 33 × 8 + 4 + 4 = 40400 мм

437 деталей · 253.87 м²

Висота: 7 × 1250 + 661 + 7 × 8 + 4 + 4 = 9475 мм


Попереджень стіни: 61 · всі IDs у JSON

Номери у плитах: NW-NNN. Помаранчеві частини утримані від різання; перелік на арк.05.

ПдЗх / торець

Плита 1192×1250 мм · шов 8 мм · справа 432 мм | 1:60, А3 без масштабування

Рядова сітка: 1250 + 8 = 1258 мм. Ряди не збігаються автоматично з поверхами.

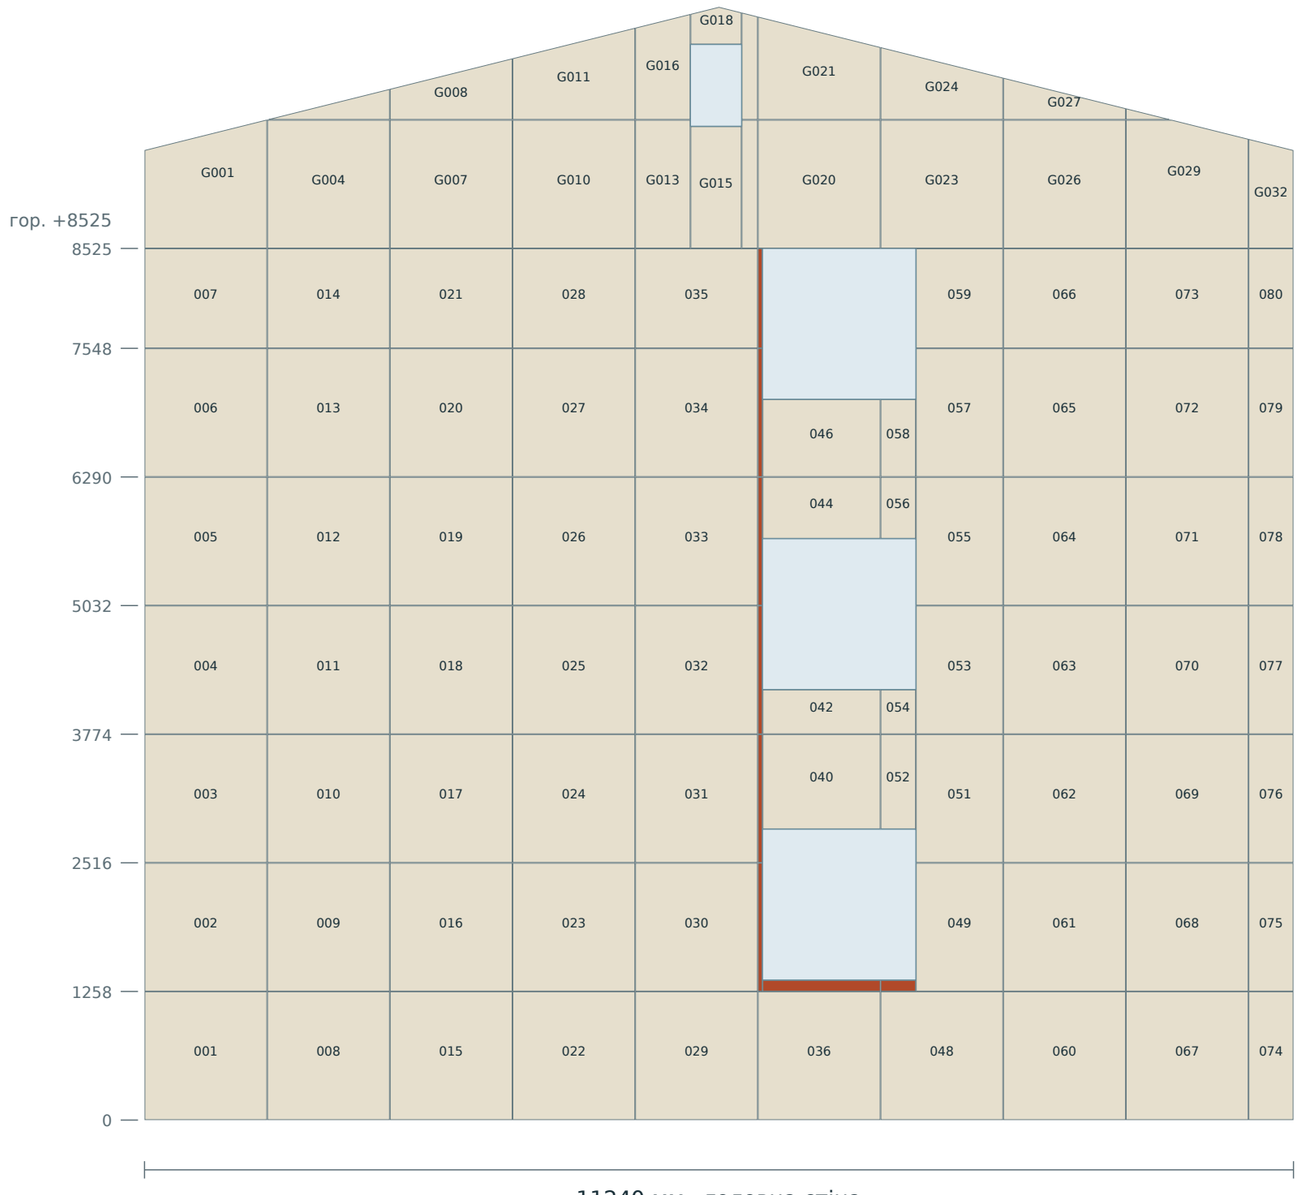

1250 мм плита

+ 8 мм шов

= 1258 мм ряд

11240 мм · головна стіна

9 × 1192 + 432 + 9 × 8 + 4 + 4 = 11240 мм

Висота: 6 × 1250 + 969 + 6 × 8 + 4 + 4 = 8525 мм

Номери у плитах: SW-NNN / SWG-NNN. Фронтон від +8525, скоси кандидатні.


102 деталей · 105.81 м²

Попереджень стіни: 8 · всі IDs у JSON

ПнСх / торець

Плита 1192×1250 мм · шов 8 мм · справа 432 мм | 1:60, А3 без масштабування

Рядова сітка: 1250 + 8 = 1258 мм. Ряди не збігаються автоматично з поверхами.

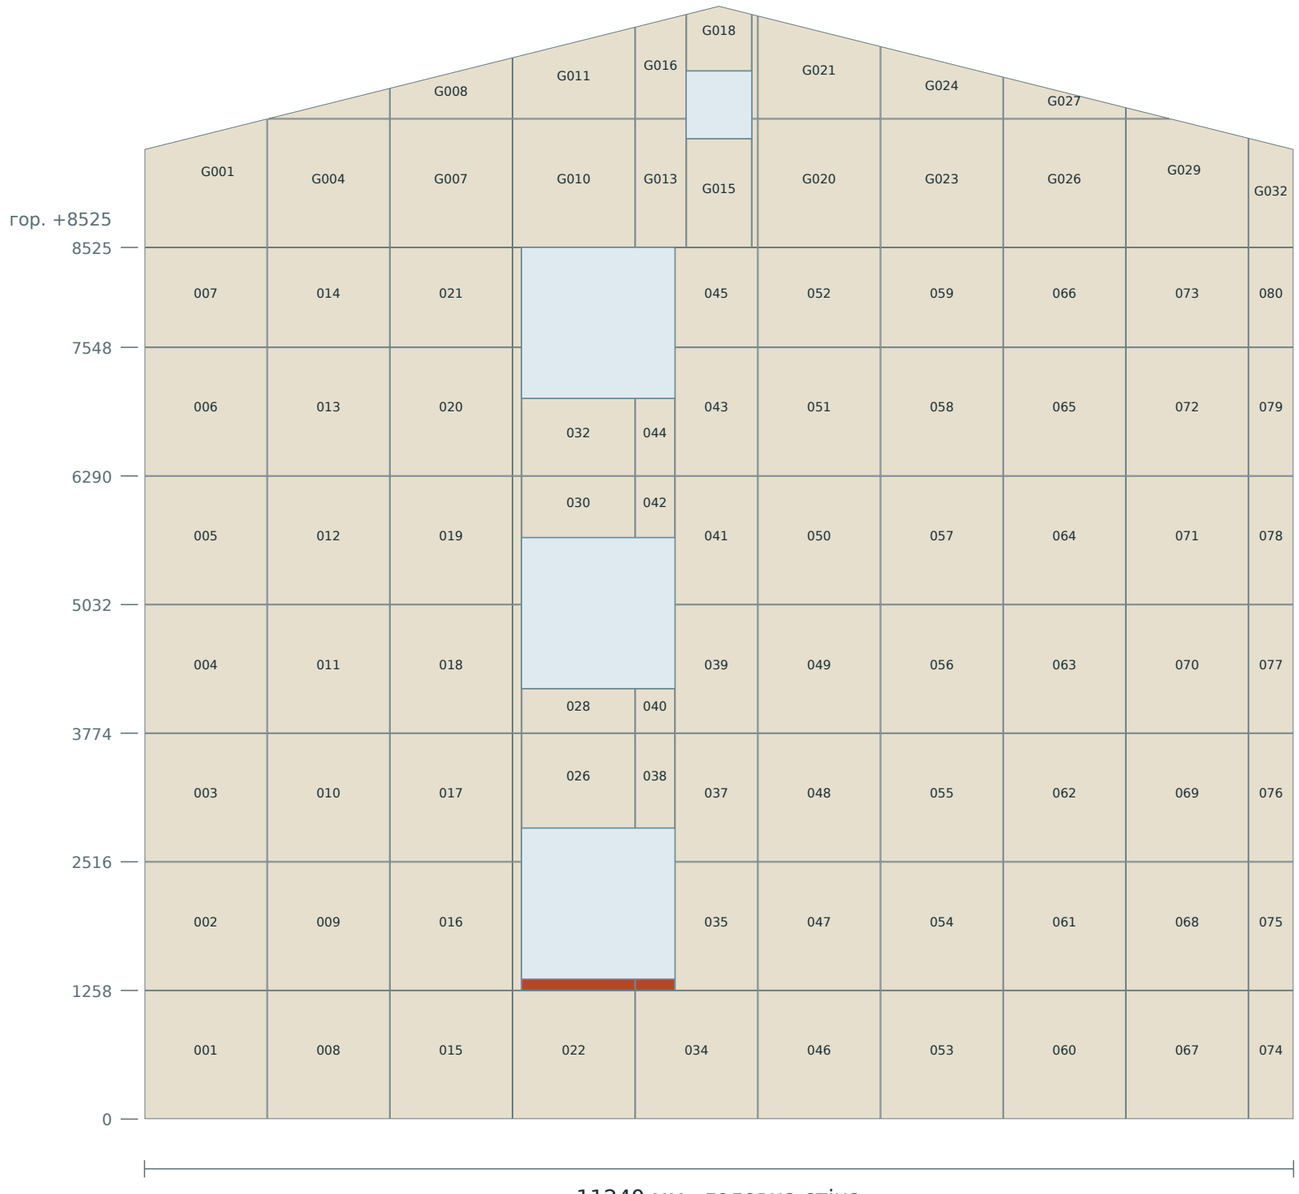

1250 мм плита

+ 8 мм шов

= 1258 мм ряд

9 × 1192 + 432 + 9 × 8 + 4 + 4 = 11240 мм

Висота: 6 × 1250 + 969 + 6 × 8 + 4 + 4 = 8525 мм

Номери у плитах: NE-NNN / NEG-NNN. Фронтон від +8525, скоси кандидатні.

102 деталей · 105.78 м²

Попереджень стіни: 2 · всі IDs у JSON

Підсумок і утримані деталі

Чотири головні стіни + два фронтони. Це відомість геометрії; не закупівля й не допуск до різання.

1090 деталей = 1046 прямокутних + 44 профільованих

571 лист - евристичне пакування; не замовлення. Пропил 3 мм, крайове обрізання 0 мм - сценарій.

Чиста геометрична площа 768.38 м²; заготовки 771.19 м²; видалення скосами 2.81 м².

Нерозподілено 79.60 м² = залишки-кандидати 76.54 + прямокутний пропил 3.06; це не фактичні відходи.

ФАСАД	ДЕТАЛЕЙ	ПЛОЩА, м²	ВУЗЬКІ / КОРОТКІ	ПРАВИЙ ЗАЛИШОК
SE / ПдСх / входи	449	302.91	36	792 мм
NW / ПнЗх / балкони	437	253.87	61	792 мм
SW / ПдЗх / торець	80	87.84	8	432 мм
NE / ПнСх / торець	80	87.84	2	432 мм
SWG / ПдЗх / фронтон	22	17.96	скоси: окрема звірка	432 мм
NEG / ПнСх / фронтон	22	17.94	скоси: окрема звірка	432 мм

107 фасадних деталей з геометричними попередженнями - CSV для різання УТРИМАНО

ID / ширина×висота, мм. 50 мм ширини і 160 мм висоти - необхідні фільтри, не інженерне погодження.

SE-003 277×103	SE-347 32×1250	NW-102 2×1250	NW-301 1192×46
SE-016 1192×103	SE-350 392×42	NW-111 371×46	NW-303 1192×47
SE-025 287×103	SE-354 32×1250	NW-123 851×46	NW-314 372×46
SE-048 392×74	SE-357 32×1250	NW-124 333×46	NW-316 712×46
SE-056 392×42	SE-391 392×74	NW-127 851×47	NW-320 372×47
SE-097 392×74	SE-397 392×42	NW-138 943×46	NW-328 231×103
SE-103 392×42	SE-416 446×103	NW-141 943×47	NW-341 1192×103
SE-122 809×103	SE-429 1192×103	NW-152 123×46	NW-350 333×103
SE-136 955×103	SE-438 118×103	NW-155 123×47	NW-364 761×103
SE-150 229×103	NW-008 61×46	NW-162 1192×46	NW-378 1003×103
SE-163 1192×103	NW-011 61×47	NW-164 1192×47	NW-396 453×46
SE-172 335×103	NW-018 1192×46	NW-172 471×46	NW-408 933×46
SE-193 22×1250	NW-020 1192×47	NW-173 712×46	NW-409 251×46
SE-195 392×74	NW-028 533×46	NW-176 471×47	NW-412 933×47
SE-200 22×1250	NW-029 651×46	NW-182 131×103	NW-423 861×46
SE-203 392×42	NW-032 533×47	NW-195 1192×103	NW-426 861×47
SE-207 22×1250	NW-039 52×103	NW-204 433×103	SW-037 38×1250
SE-210 22×1250	NW-044 53×46	NW-218 661×103	SW-038 1146×104
SE-244 392×74	NW-056 1192×103	NW-232 1103×103	SW-039 38×1250
SE-250 392×42	NW-065 512×103	NW-250 471×46	SW-041 38×1250
SE-269 826×103	NW-079 582×103	NW-262 951×46	SW-043 38×1250
SE-283 938×103	NW-092 2×1250	NW-263 233×46	SW-045 38×1250
SE-297 247×103	NW-093 1182×103	NW-266 951×47	SW-047 38×969
SE-310 1192×103	NW-094 2×1250	NW-277 843×46	SW-050 338×104
SE-319 317×103	NW-096 2×1250	NW-280 843×47	NE-024 1103×104
SE-340 32×1250	NW-098 2×1250	NW-291 222×46	NE-036 381×104
SE-342 392×74	NW-100 2×1250	NW-294 222×47	

44 профільовані деталі фронтонів: контур, опори, кріплення й операції довершення також залишаються кандидатами.

Джерело IDs: Mäe7-фасад-розкрій-v19.json. Без цоколя, відкосів, балконів, навісів і даху.

Ціла заготовка з вирізом - тільки порівняння


Реальна комірка SE-GRID-C001-R003, проріз SE-W01. Не додається до кількостей чи native.

Patina WOOD DIM rev02.2026, p17: рекомендує окремі секції біля прорізів.

Гострі внутрішні кути, радіуси, кріплення й виробничий допуск цілого вирізу тут не погоджені.

Поточний E: 2 секції

1250 мм / 1:10 · 4 мм до прорізу

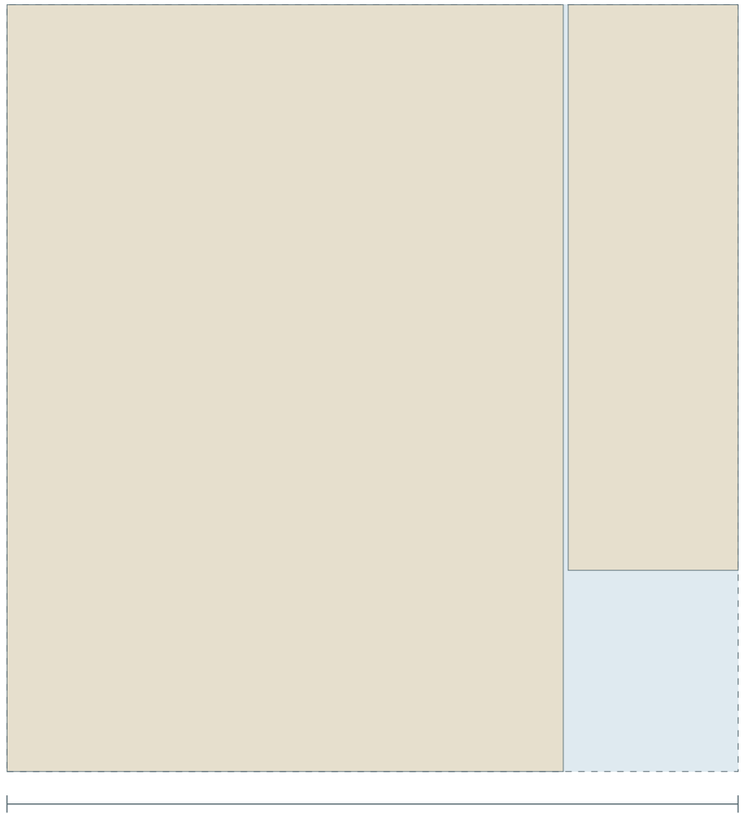


1192 мм · початкова готова плита

IDs: SE-004, SE-005

2 дет. / 1.38914 м² збереженої геометрії

Порівняння: одна Г-подібна деталь

1250 мм / 1:10 · 4 мм до прорізу

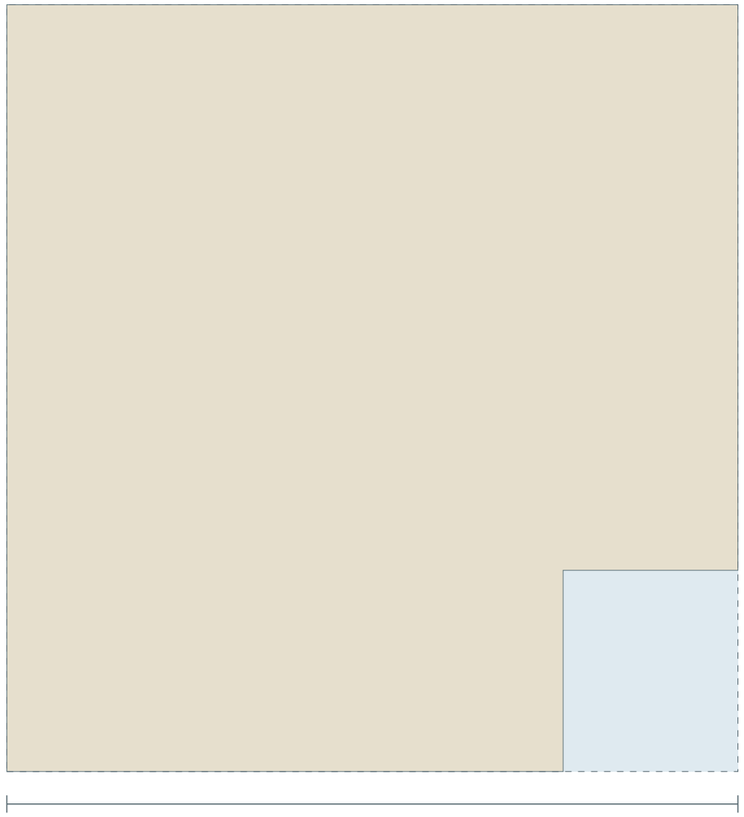

1192 мм · початкова готова плита

IDs: SE-GRID-C001-R003-C01

1 дет. / 1.39652 м² збереженої геометрії

Пунктир - початкова заготовка. Блакитне - вилучений матеріал. Праворуч немає зайвого шва між секціями.

Різниця площі виникає від шва між прямокутними секціями; це не доказ економії, міцності чи придатності вирізу.
APPROVED=false · READY TO CUT=false · порівняльні IDs не замінюють відомість 1090 деталей.