
ПдСх / входи

Плита 1192×1250 мм · шов 8 мм · справа 792 мм | 1:125, А3 без масштабування


Спільні горизонтальні Y: 0 / 1113 / 2371 / 3629 / 4887 / 6009 / 7267 / 8525 / 9475 мм; висота плити ≤1250 мм.

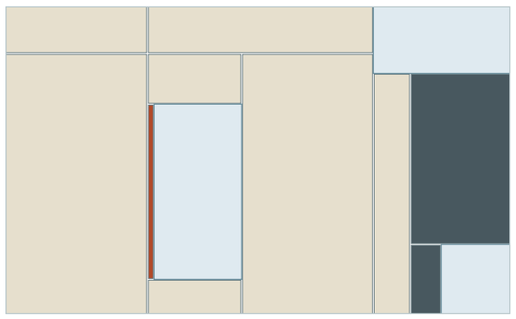


SE-185: 22×792 мм / 1:28



SE-191: 22×697 мм / 1:28

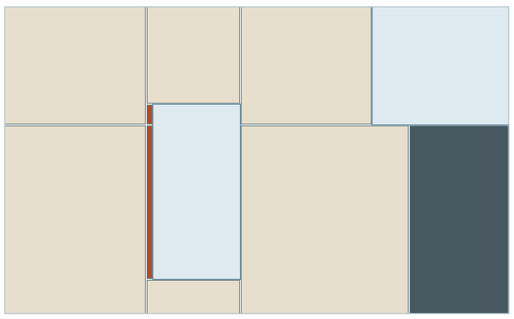

SE-192: 22×87 мм / 1:28

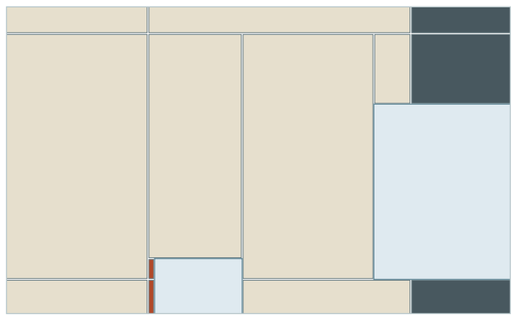

33 × 1192 + 792 + 33 × 8 + 4 + 4 = 40400 мм

424 деталей · 303.27 м²

Висота: 1105 + 1250 + 1250 + 1250 + 1114 + 1250 + 1250 + 942 + 7 × 8 + 4 + 4 = 9475 мм


Попереджень стіни: 10 · всі IDs у JSON

Номери у плитах: SE-NNN. Помаранчеві частини утримані від різання; перелік на арк.05.


ПнЗх / балкони

Плита 1192×1250 мм · шов 8 мм · справа 792 мм | 1:125, А3 без масштабування


Спільні горизонтальні Y: 0 / 1113 / 2371 / 3629 / 4887 / 6009 / 7267 / 8525 / 9475 мм; висота плити ≤1250 мм.

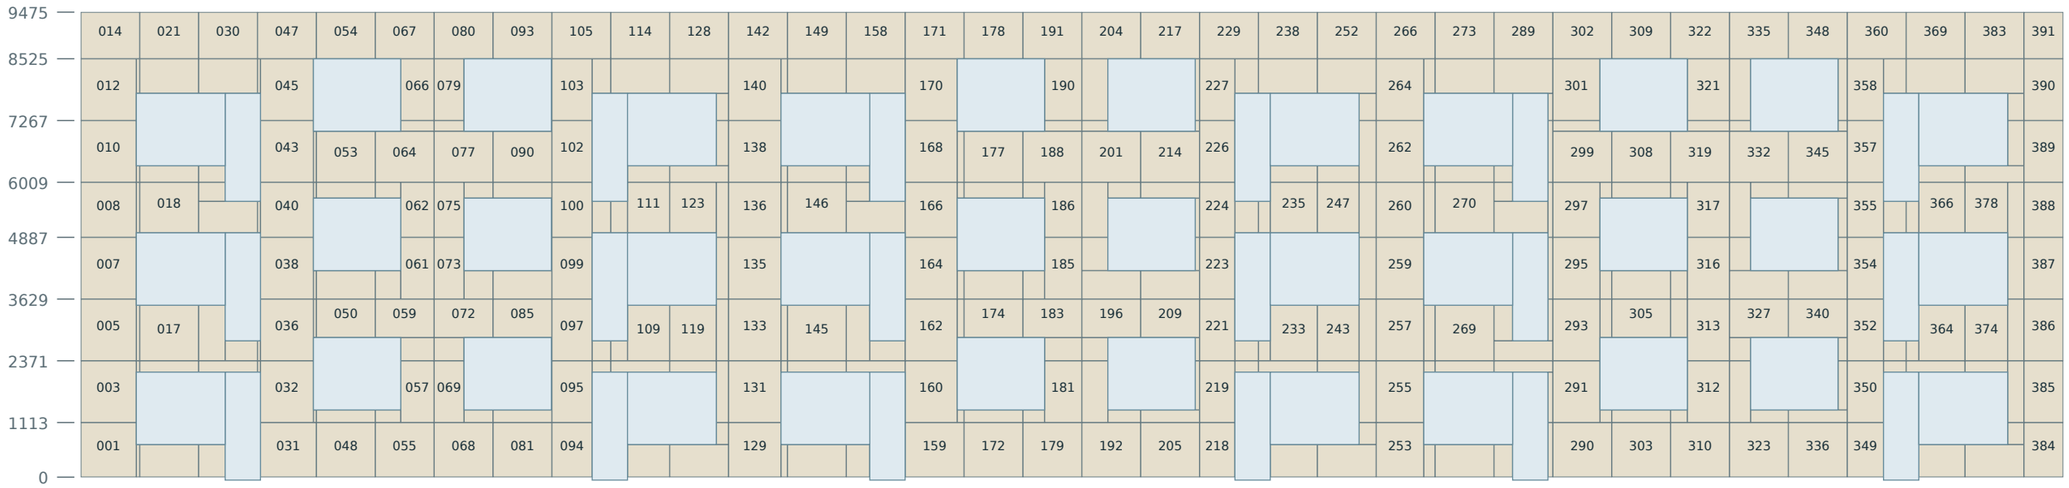


NW-083: 2×994 мм / 1:28

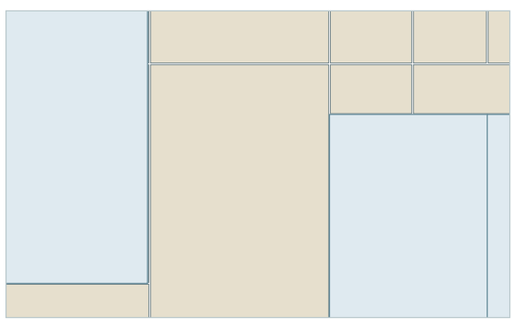

NW-084: 2×465 мм / 1:28

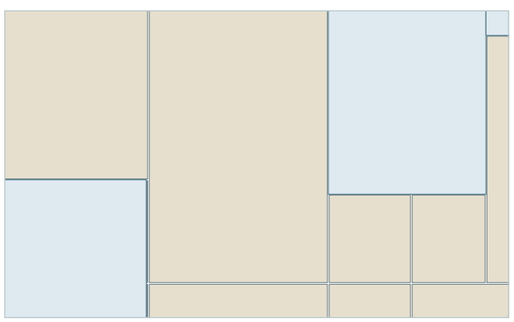

NW-087: 2×670 мм / 1:28

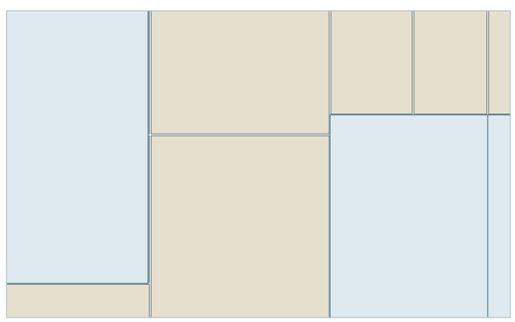

33 × 1192 + 792 + 33 × 8 + 4 + 4 = 40400 мм

391 деталей · 254.22 м²

Висота: 1105 + 1250 + 1250 + 1250 + 1114 + 1250 + 1250 + 942 + 7 × 8 + 4 + 4 = 9475 мм


Попереджень стіни: 6 · всі IDs у JSON

Номери у плитах: NW-NNN. Помаранчеві частини утримані від різання; перелік на арк.05.

ПдЗх / торець

Плита 1192×1250 мм · шов 8 мм · справа 432 мм | 1:60, А3 без масштабування

Спільні горизонтальні Y: 0 / 1113 / 2371 / 3629 / 4887 / 6009 / 7267 / 8525 мм; висота плити ≤1250 мм.

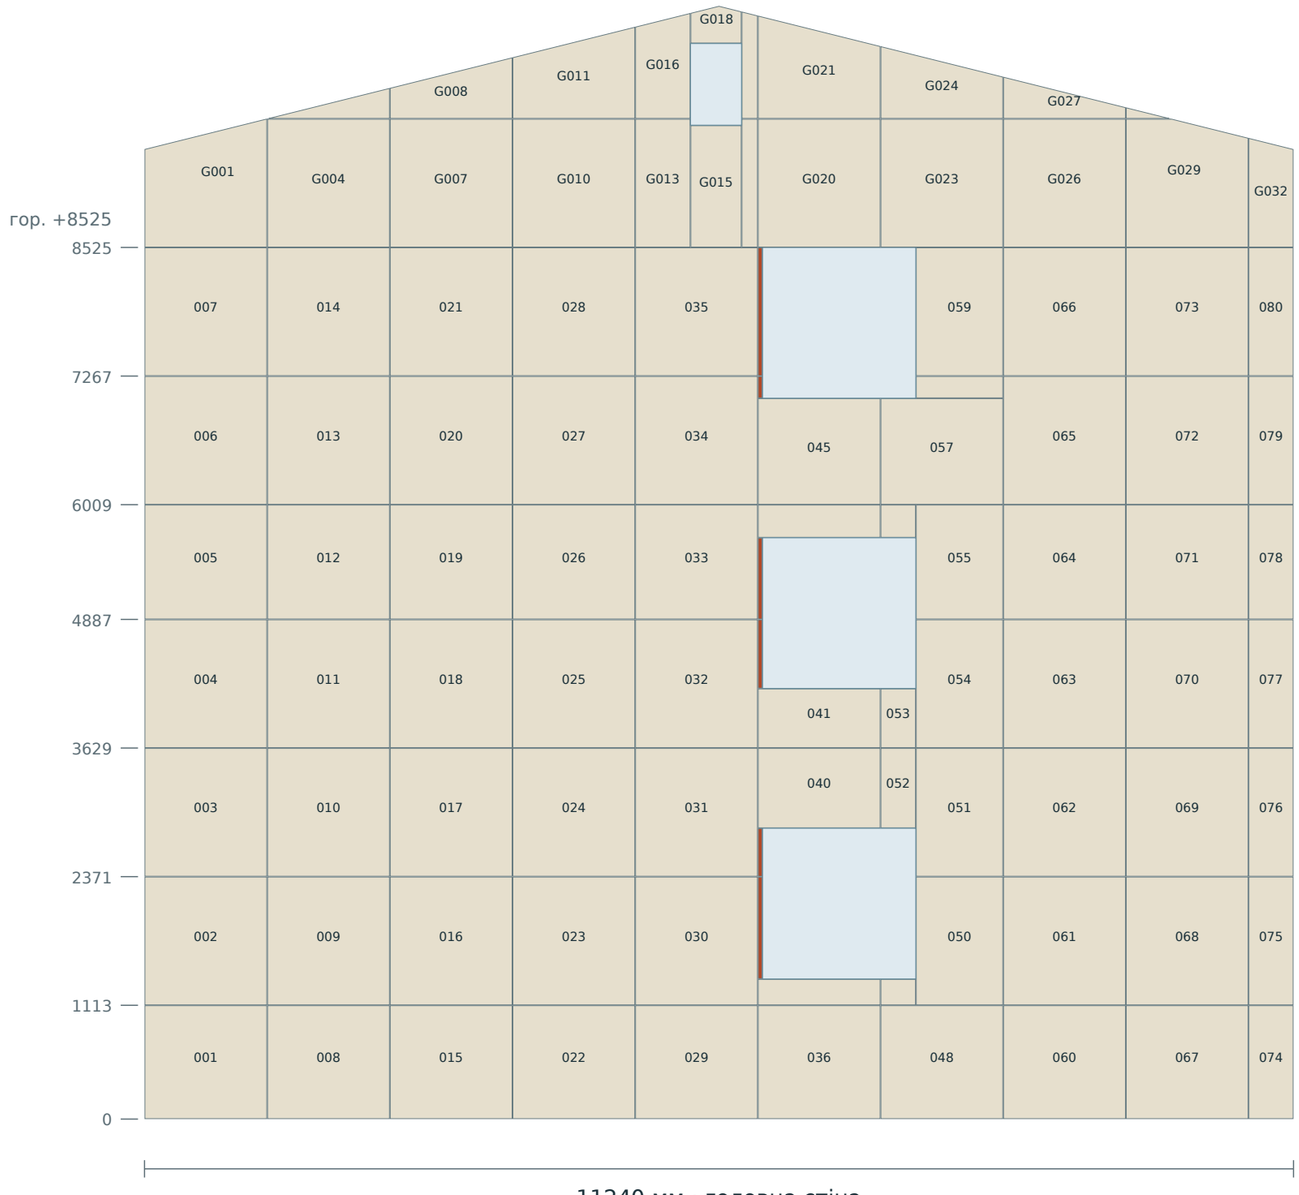

висота ≤1250 мм

+ 8 мм шов

= ≤1258 мм ряд

9 × 1192 + 432 + 9 × 8 + 4 + 4 = 11240 мм

Висота: 1105 + 1250 + 1250 + 1250 + 1114 + 1250 + 1250 + 6 × 8 + 4 + 4 = 8525 мм

Номери у плитах: SW-NNN / SWG-NNN. Фронтон від +8525, скоси кандидатні.


102 деталей · 105.83 м²

Попереджень стіни: 6 · всі IDs у JSON

ПнСх / торець

Плита 1192×1250 мм · шов 8 мм · справа 432 мм | 1:60, А3 без масштабування

Спільні горизонтальні Y: 0 / 1113 / 2371 / 3629 / 4887 / 6009 / 7267 / 8525 мм; висота плити ≤1250 мм.

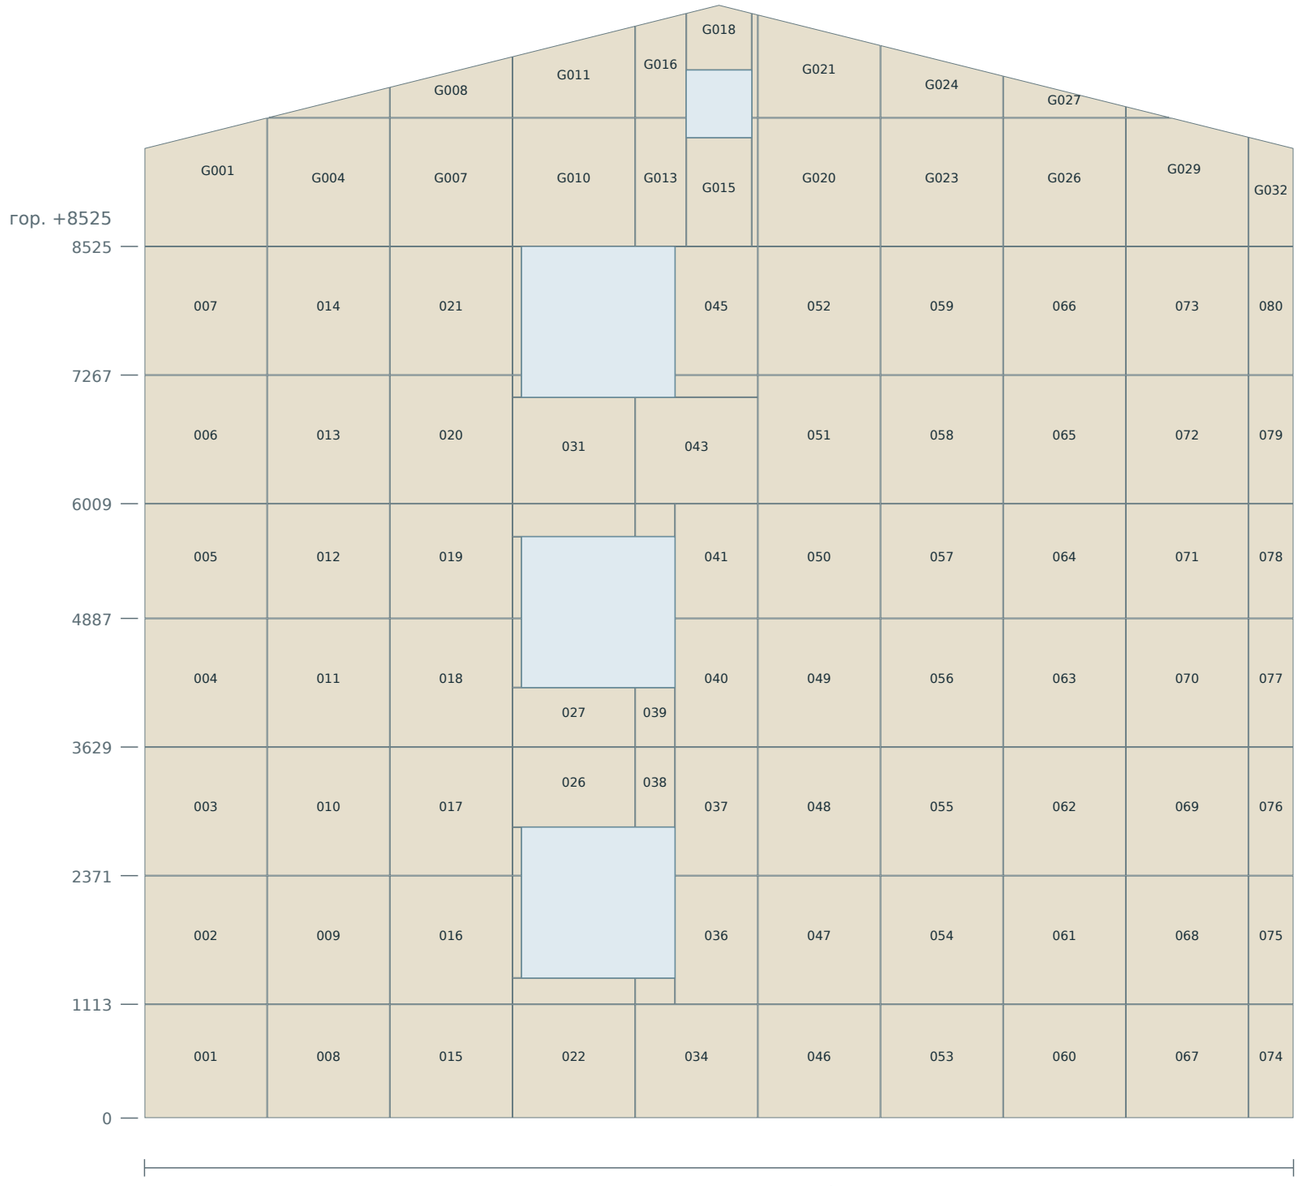

11240 мм · головна стіна

висота ≤1250 мм

+ 8 мм шов

= ≤1258 мм ряд

9 × 1192 + 432 + 9 × 8 + 4 + 4 = 11240 мм

Висота: 1105 + 1250 + 1250 + 1250 + 1114 + 1250 + 1250 + 6 × 8 + 4 + 4 = 8525 мм

Номери у плитах: NE-NNN / NEG-NNN. Фронтон від +8525, скоси кандидатні.

102 деталей · 105.80 м²

Попереджень стіни: 0 · всі IDs у JSON

Підсумок і утримані деталі

Чотири головні стіни + два фронтони. Це відомість геометрії; не закупівля й не допуск до різання.

1019 деталей = 975 прямокутних + 44 профільованих

567 листів - евристичне пакування; не оптимум чи замовлення. Пропил 3 мм, обрізання 0 мм - сценарій.

Чиста геометрична площа 769.12 м²; заготовки 771.93 м²; видалення скосами 2.81 м².

Нерозподілено 72.90 м² = залишки-кандидати 69.76 + прямокутний пропил 3.13; це не фактичні відходи.

ФАСАД	ДЕТАЛЕЙ	ПЛОЩА, м²	ВУЗЬКІ / КОРОТКІ	ПРАВИЙ ЗАЛИШОК
SE / ПдСх / входи	424	303.27	10	792 мм
NW / ПнЗх / балкони	391	254.22	6	792 мм
SW / ПдЗх / торець	80	87.86	6	432 мм
NE / ПнСх / торець	80	87.86	0	432 мм
SWG / ПдЗх / фронтон	22	17.96	скоси: окрема звірка	432 мм
NEG / ПнСх / фронтон	22	17.94	скоси: окрема звірка	432 мм

4 стіни: 746401500 = 733218560 збережено + 13155040 шви + 27900 поглинуто, мм² (39 смуг).

22 утримані деталі: ширина 22, висота 2 (перетин категорій). CSV УТРИМАНО.

Ш <50 / В <160 мм - консервативний сценарій, не універсальна заборона виробника. Patina p17: звірити умови малих дощок 100–150 мм.

SE-185 22×792 Ш	SE-330 32×697 Ш	NW-087 2×670 Ш	SW-042 38×668 Ш
SE-191 22×697 Ш	SE-331 32×87 Ш/В	NW-088 2×789 Ш	SW-043 38×791 Ш
SE-192 22×87 Ш/В	SE-336 32×239 Ш	NW-091 2×210 Ш	SW-046 38×209 Ш
SE-197 22×239 Ш	SE-338 32×545 Ш	NW-092 2×1250 Ш	SW-047 38×1250 Ш
SE-199 22×545 Ш	NW-083 2×994 Ш	SW-038 38×993 Ш	
SE-324 32×792 Ш	NW-084 2×465 Ш	SW-039 38×466 Ш	

44 профільовані деталі фронтонів: контур, опори, кріплення й операції довершення також залишаються кандидатами.
Джерело IDs: Mäe7-фасад-розкрій-v20.json. Без цоколя, відкосів, балконів, навісів і даху.

Ціла заготовка з вирізом - тільки порівняння


Реальна комірка SE-GRID-C001-R002, проріз SE-W01. Не додається до кількостей чи native.

Patina WOOD DIM rev02.2026, p17: рекомендує окремі секції біля прорізів.

Гострі внутрішні кути, радіуси, кріплення й виробничий допуск цілого вирізу тут не погоджені.

Поточний E: 2 секції

1250 мм / 1:10 · 4 мм до прорізу

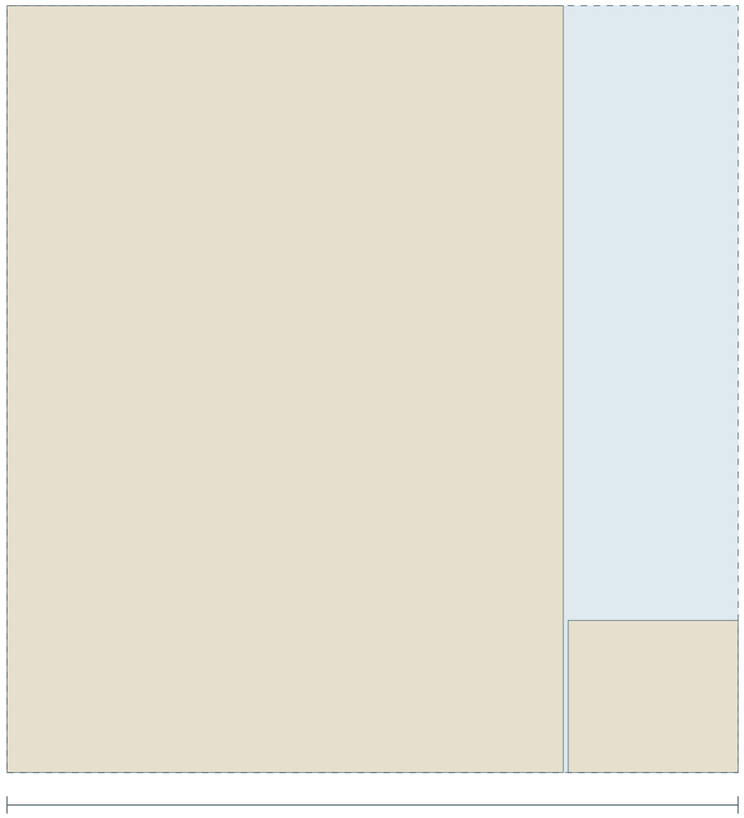


1192 мм · початкова готова плита

IDs: SE-002, SE-003

2 дет. / 1.20245 м² збереженої геометрії

Порівняння: одна Г-подібна деталь

1250 мм / 1:10 · 4 мм до прорізу

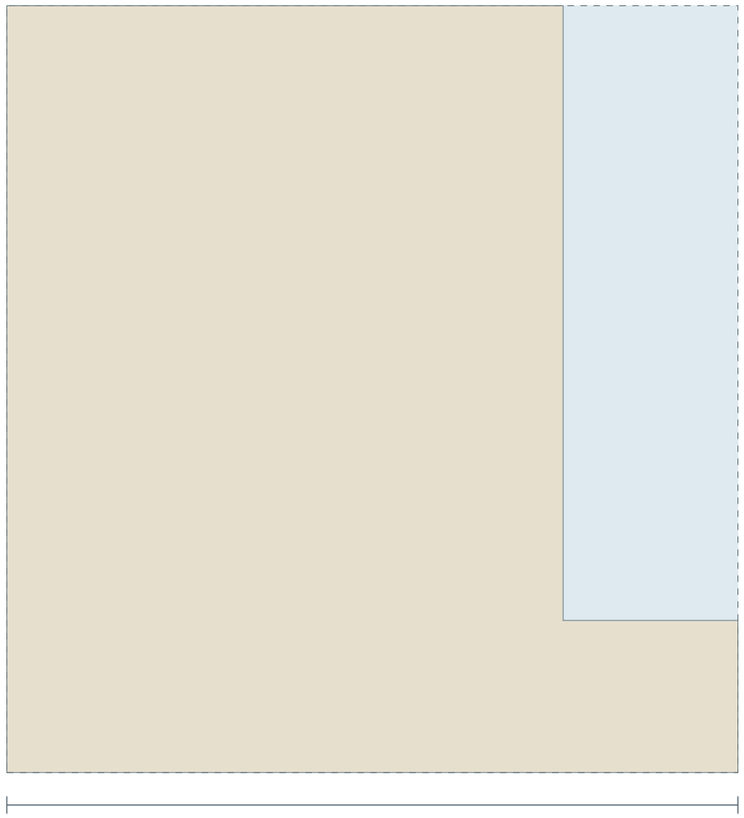

1192 мм · початкова готова плита

IDs: SE-GRID-C001-R002-C01

1 дет. / 1.20443 м² збереженої геометрії

Пунктир - початкова заготовка. Блакитне - вилучений матеріал. Праворуч немає зайвого шва між секціями.

Різниця площі виникає від шва між прямокутними секціями; це не доказ економії, міцності чи придатності вирізу.
APPROVED=false · READY TO CUT=false · порівняльні IDs не замінюють відомість 1019 деталей.